


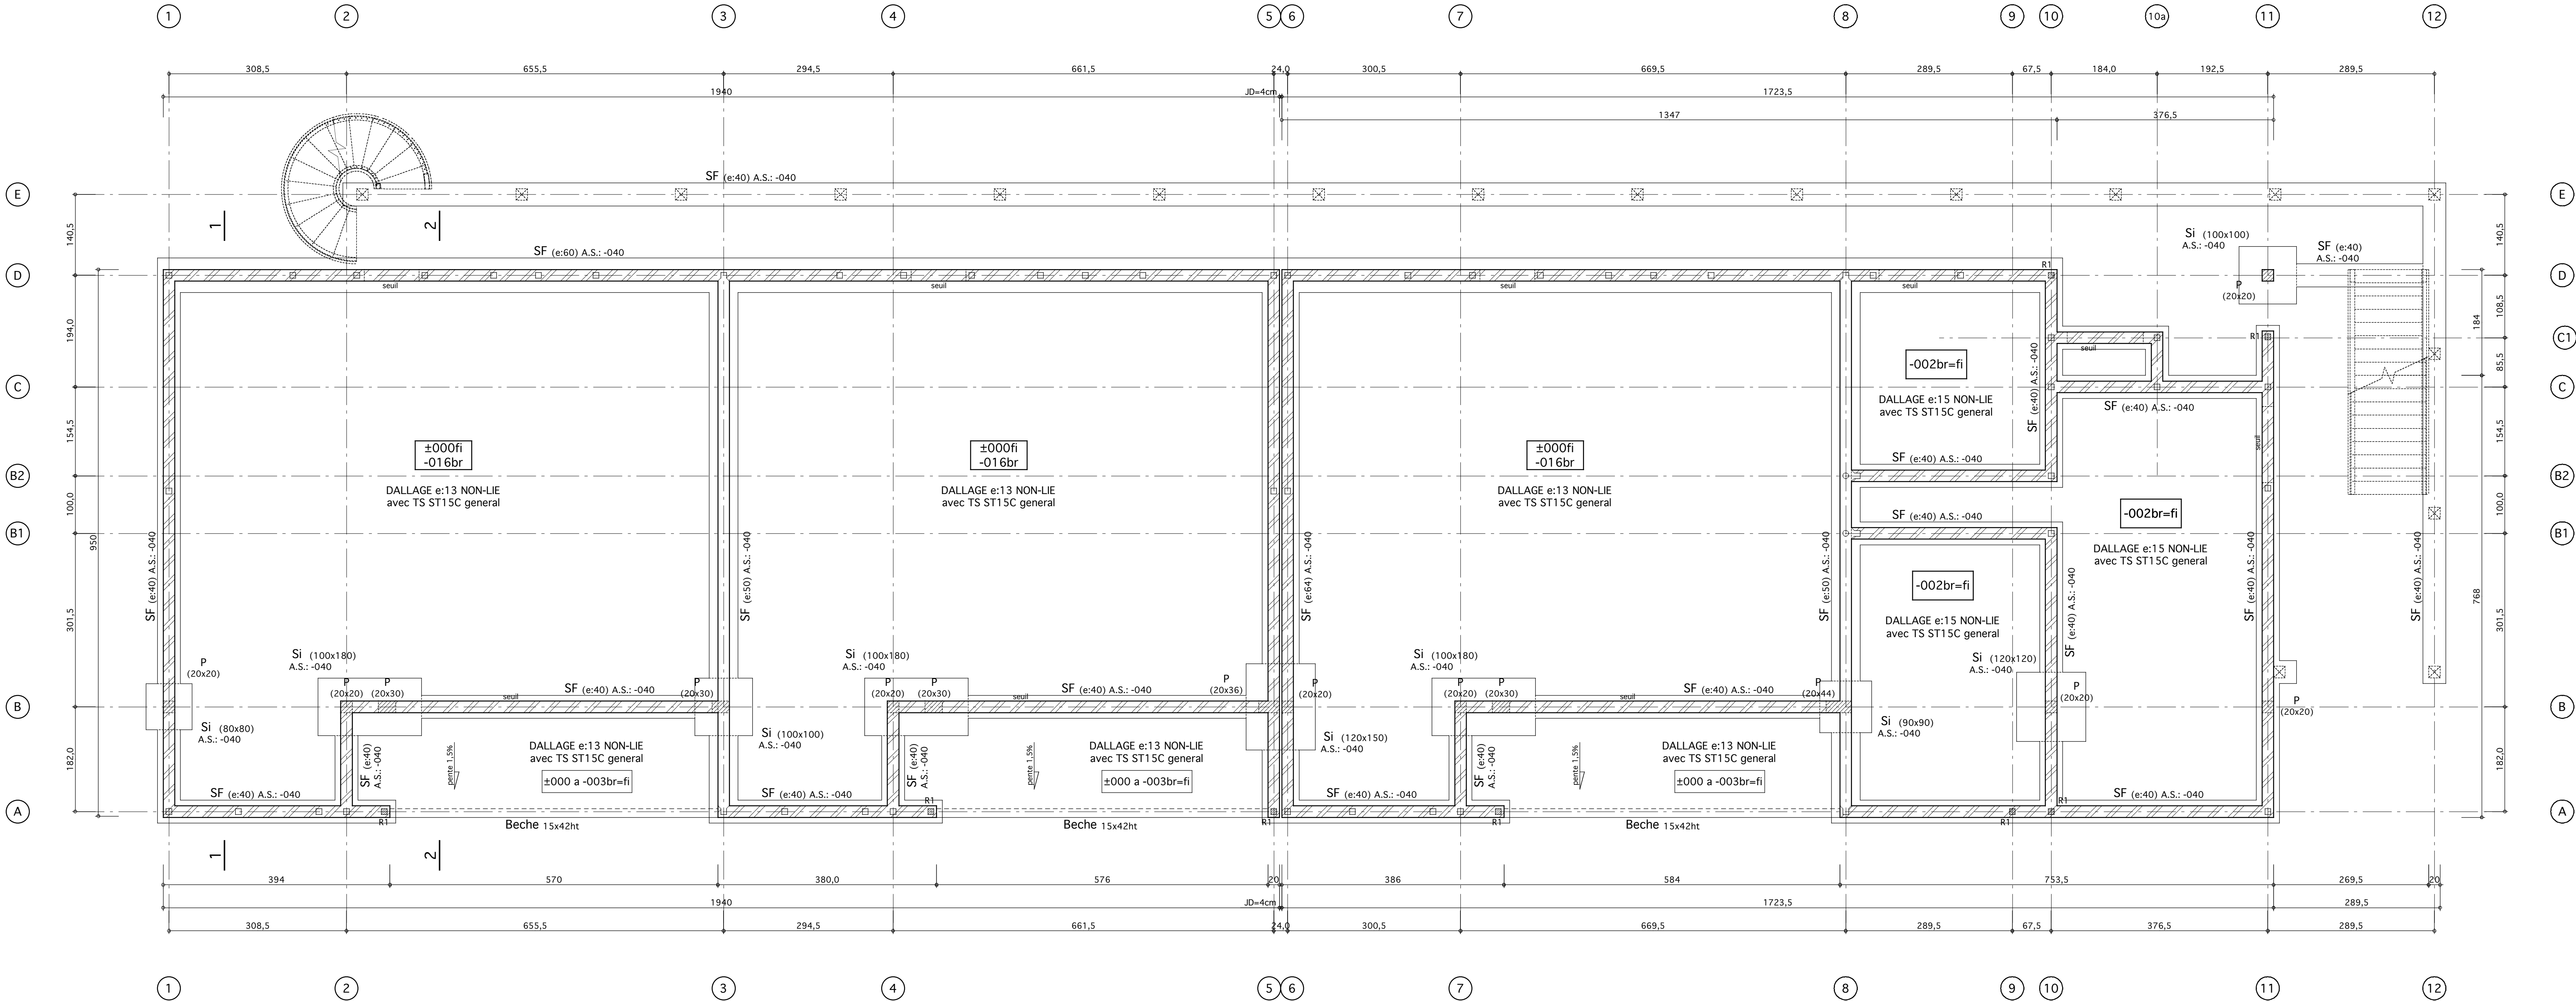

CONTRAINTE ADMISSIBLE DU SOL qELS= 0,25 MPa

- FONDATIONS:
FONDATIONS SUPERFICIELLES DE TYPE SEMELLES FILANTES/ISOLEES, ANCREES D'AU MOINS 15cm DANS LES MATERIAUX FLUVIO-GLACIAIRES (sol n°2), D'OU DES ENCASTREMENTS COMPRIS ENTRE 0.75 et 1,35m/TN AU DROIT DES SONDAGES. RESPECTER LES SUJETIONS D'EXECUTION PRECISES DANS LE RAPPORT GEOTECHNIQUE.
ARASE SUPERIEURE: Cf vue en plan
Cf: Etude Geotechnique de SOL INGENIERIE n°18.10.158

- MUR BANCHE (e:20)
- 1 RANG BLOC U (e:20) avec CH 4HA10 FILANTS + 1 RANG MIN. BLOC PLEINS ALLEGES (cf vue en plan)
- ATTENTES RAIDISSEURS: ARMATURES 4HA10+cad. HA6 e:10
- ATTENTES RAIDISSEURS ARMES: ARMATURES 4HA12+cad. HA6 e:10

HYPOTHESES SISMIQUES:
. Ferrieres situe en zone sismique 3: $a_g=1,1m/s^{-2}$
. Batiment categorie d'importance 2: $\gamma=1$
. Sol classe E: S=1,8

D.C.E

commune: FERRIERES	departement: 09	Aff.: 134/18
AFFAIRE : HLM DE L'ARIEGE CONSTRUCTION de 11 LOGEMENTS "Coeur de Bourg"	ACIERS: fe = 500 MPa BETON: fc28 = 25 MPa ft28 = 2,1 MPa dosage suivant NF 206.1	PLAN: 01 DATE: --/06/19 ECHELLE: 1/50
DESIGNATION : FONDATIONS	modifications dates indices	EBM: "LES POUSES" Rte de Portet 31270 Villeneuve Tolosane TEL: 05.61.76.98.88 FAX: 05.61.76.79.13 [Logo]
Dessiné par : B. CHARPENTREAU	M. D'OEUVRE : Architecture & Paysage	ENT. : CONTROLE :

NOTA:
- Tous les niveaux sont donnes par rapport au ±000, qui correspond au sol fini du RDC.
- L'emprise des menuiseries sera a confirmer par le(s) lot(s) concerne(s).