


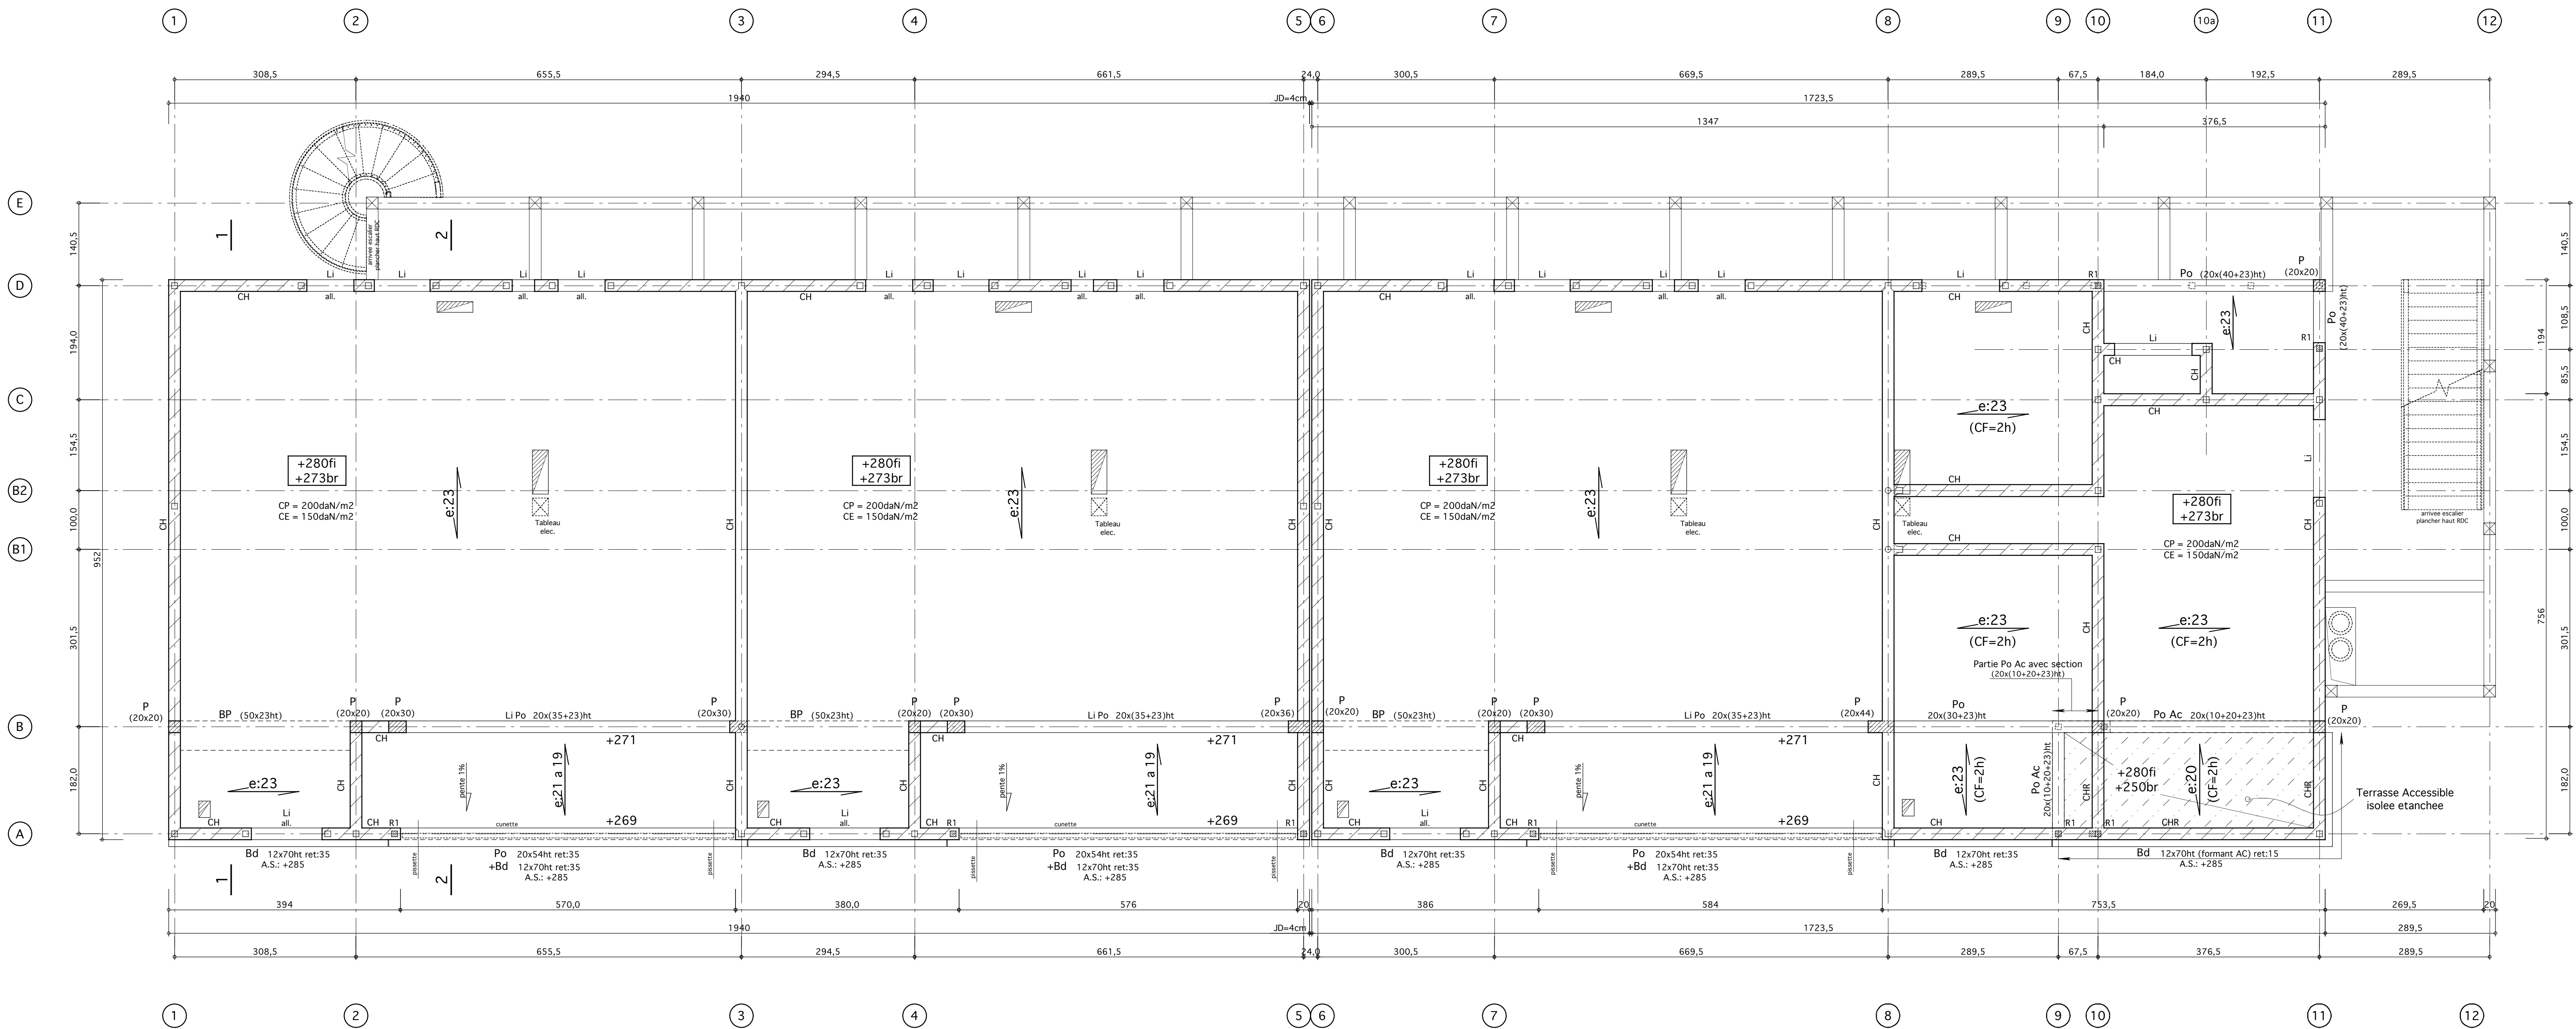

- MUR BANCHE (e:20)
- MUR MAÇONNERIE (e:20)
- RAIDISSEURS: ARMATURES 4HA10+cad. HA6 e:10
- RAIDISSEURS ARMES: ARMATURES 4HA12+cad. HA6 e:10

HYPOTHESES SISMIQUES:

- Ferrieres situe en zone sismique 3: $a_g=1,1m/s^{-2}$
- Batiment categorie d'importance 2: $\gamma=1$
- Sol classe E: $S=1,8$

$a_g=1,1m/s^{-2}$

D.C.E

commune: FERRIERES	departement: 09	Aff.: 134/18
AFFAIRE : HLM DE L'ARIEGE CONSTRUCTION de 11 LOGEMENTS "Coeur de Bourg"	ACIERS: fe = 500 MPa BETON: fc28 = 25 MPa ft28 = 2,1 MPa dosage suivant NF 206.1	PLAN: 02 DATE: --/06/19 ECHELLE: 1/50
DESIGNATION : PLANCHER HAUT RDC	modifications dates indices	EBM: "LES POUSSES" Rte de Portet 31270 Villeneuve Tolosane TEL: 05.61.76.98.88 FAX: 05.61.76.79.13
Dessiné par : B. CHARPENTREAU	M. D'OEUVRE : Architecture & Paysage	ENT. : CONTROLE :

NOTA:

- Tous les niveaux sont donnes par rapport au ± 000 , qui correspond au sol fini du RDC.
- L'emprise des menuiseries sera a confirmer par le(s) lot(s) concerne(s).