


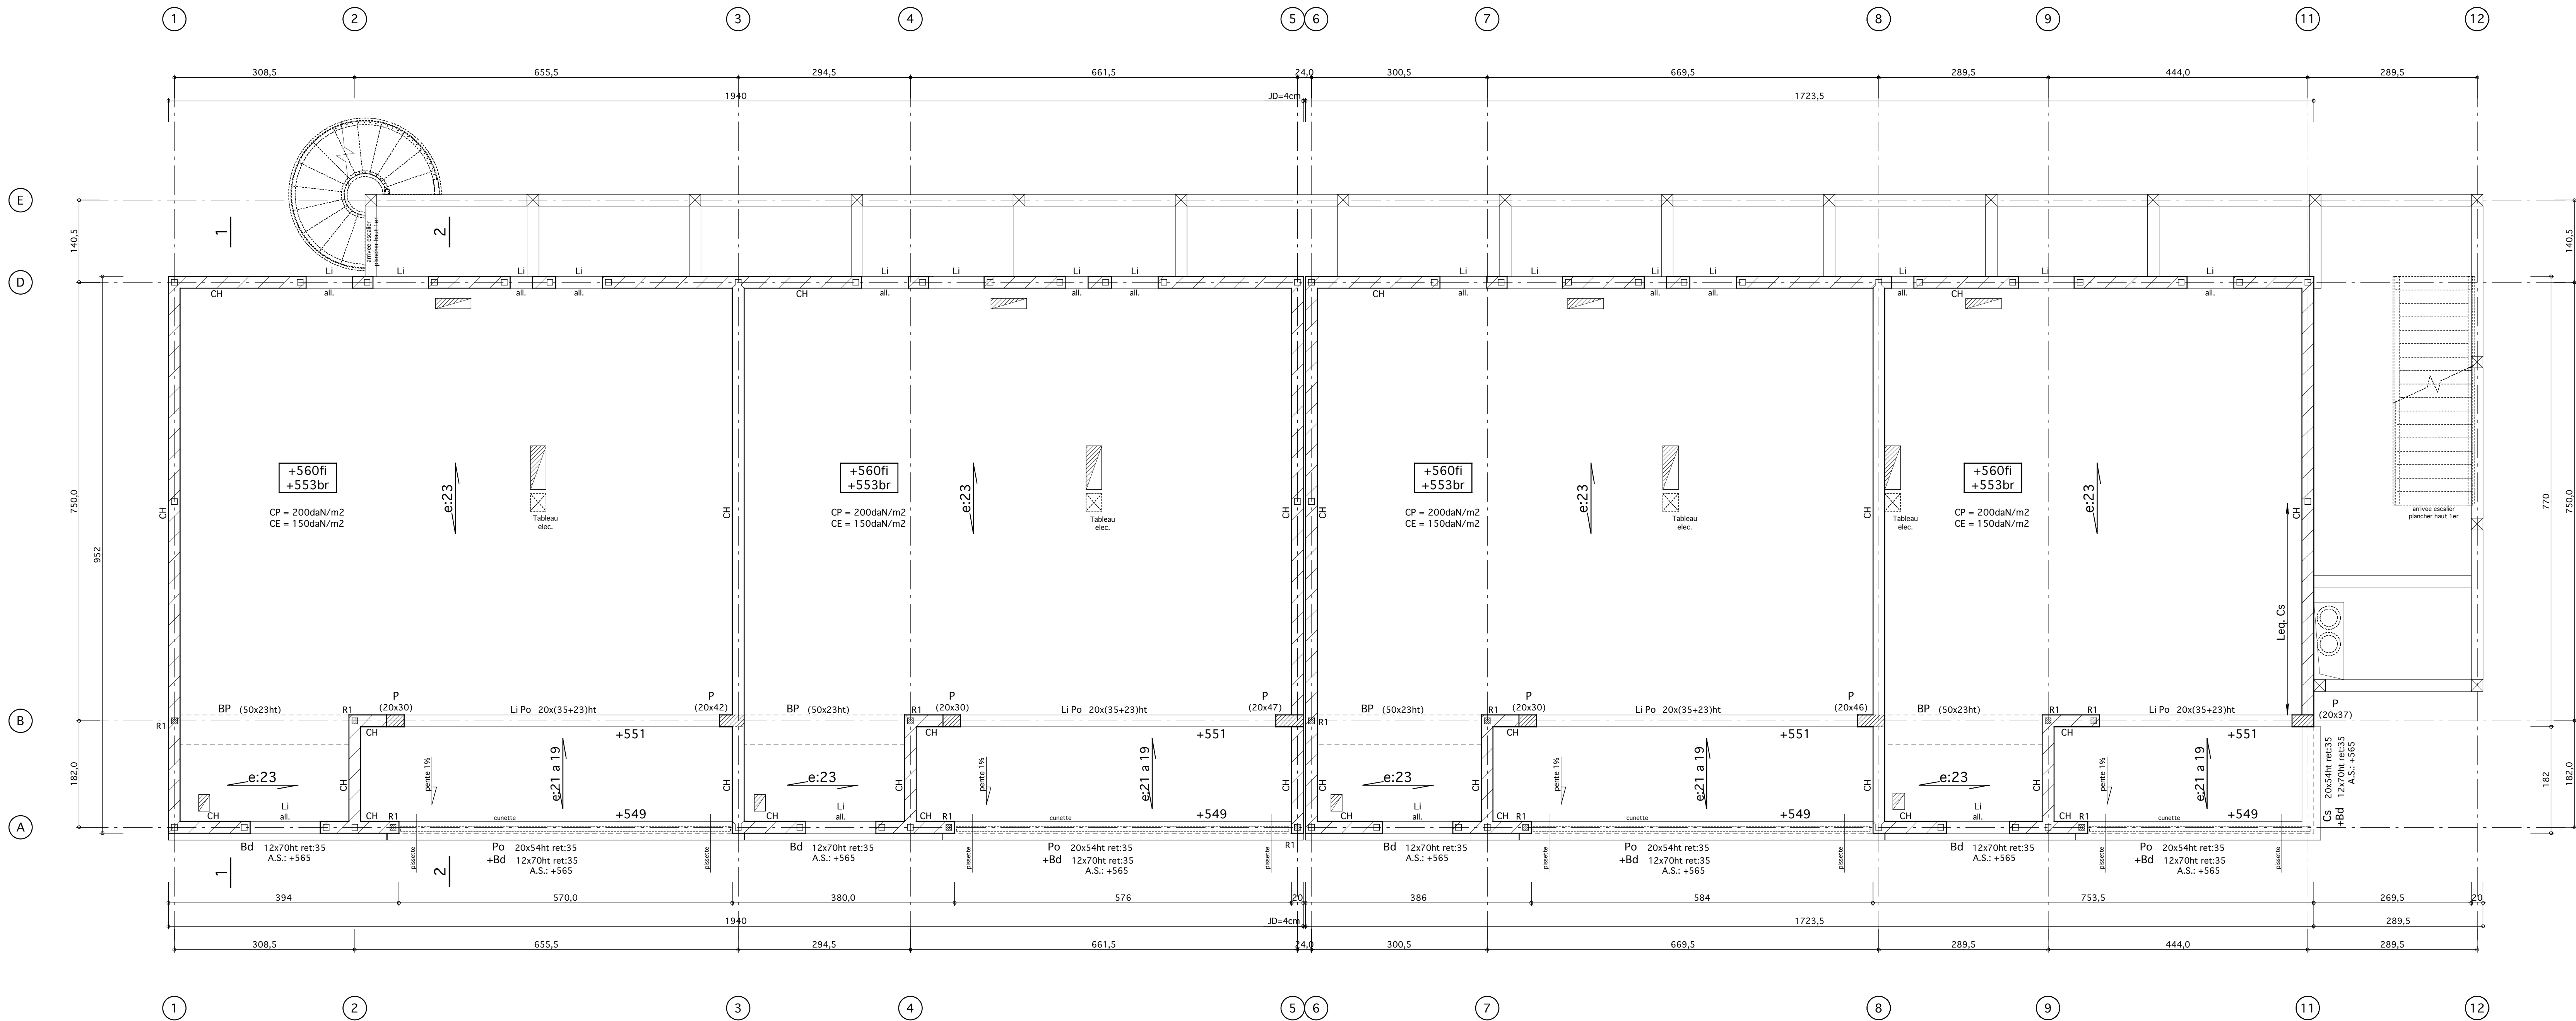

	MUR BANCHE (e:20)
	MUR MACONNERIE (e:20)
	RAIDISSEURS: ARMATURES 4HA10+cad. HA6 e:10
	RAIDISSEURS ARMES: ARMATURES 4HA12+cad. HA6 e:10

HYPOTHESES SISMIQUES:

- Ferrieres situe en zone sismique 3: $a_g=1,1m/s^{-2}$
- Batiment categorie d'importance 2: $\gamma=1$
- Sol classe E: $S=1,8$

$a_g=1,1m/s^{-2}$

D.C.E

commune: FERRIERES	departement: 09	Aff.: 134/18
AFFAIRE : HLM DE L'ARIEGE CONSTRUCTION DE 11 LOGEMENTS "Coeur de Bourg"	ACIERS: $f_e = 500$ MPa BETON: $f_{c28} = 25$ MPa $f_{t28} = 2,1$ MPa dosage suivant NF 206.1	PLAN: 03 DATE: --/06/19 ECHELLE: 1/50
DESIGNATION : PLANCHER HAUT 1ER	modifications	dates
Dessiné par : B. CHARPENTREAU	ENT. :	CONTRÔLE :
M. D'OEUVRE : Architecture & Paysage		



NOTA:

- Tous les niveaux sont donnes par rapport au ± 000 , qui correspond au sol fini du RDC.
- L'emprise des menuiseries sera a confirmer par le(s) lot(s) concerne(s).