


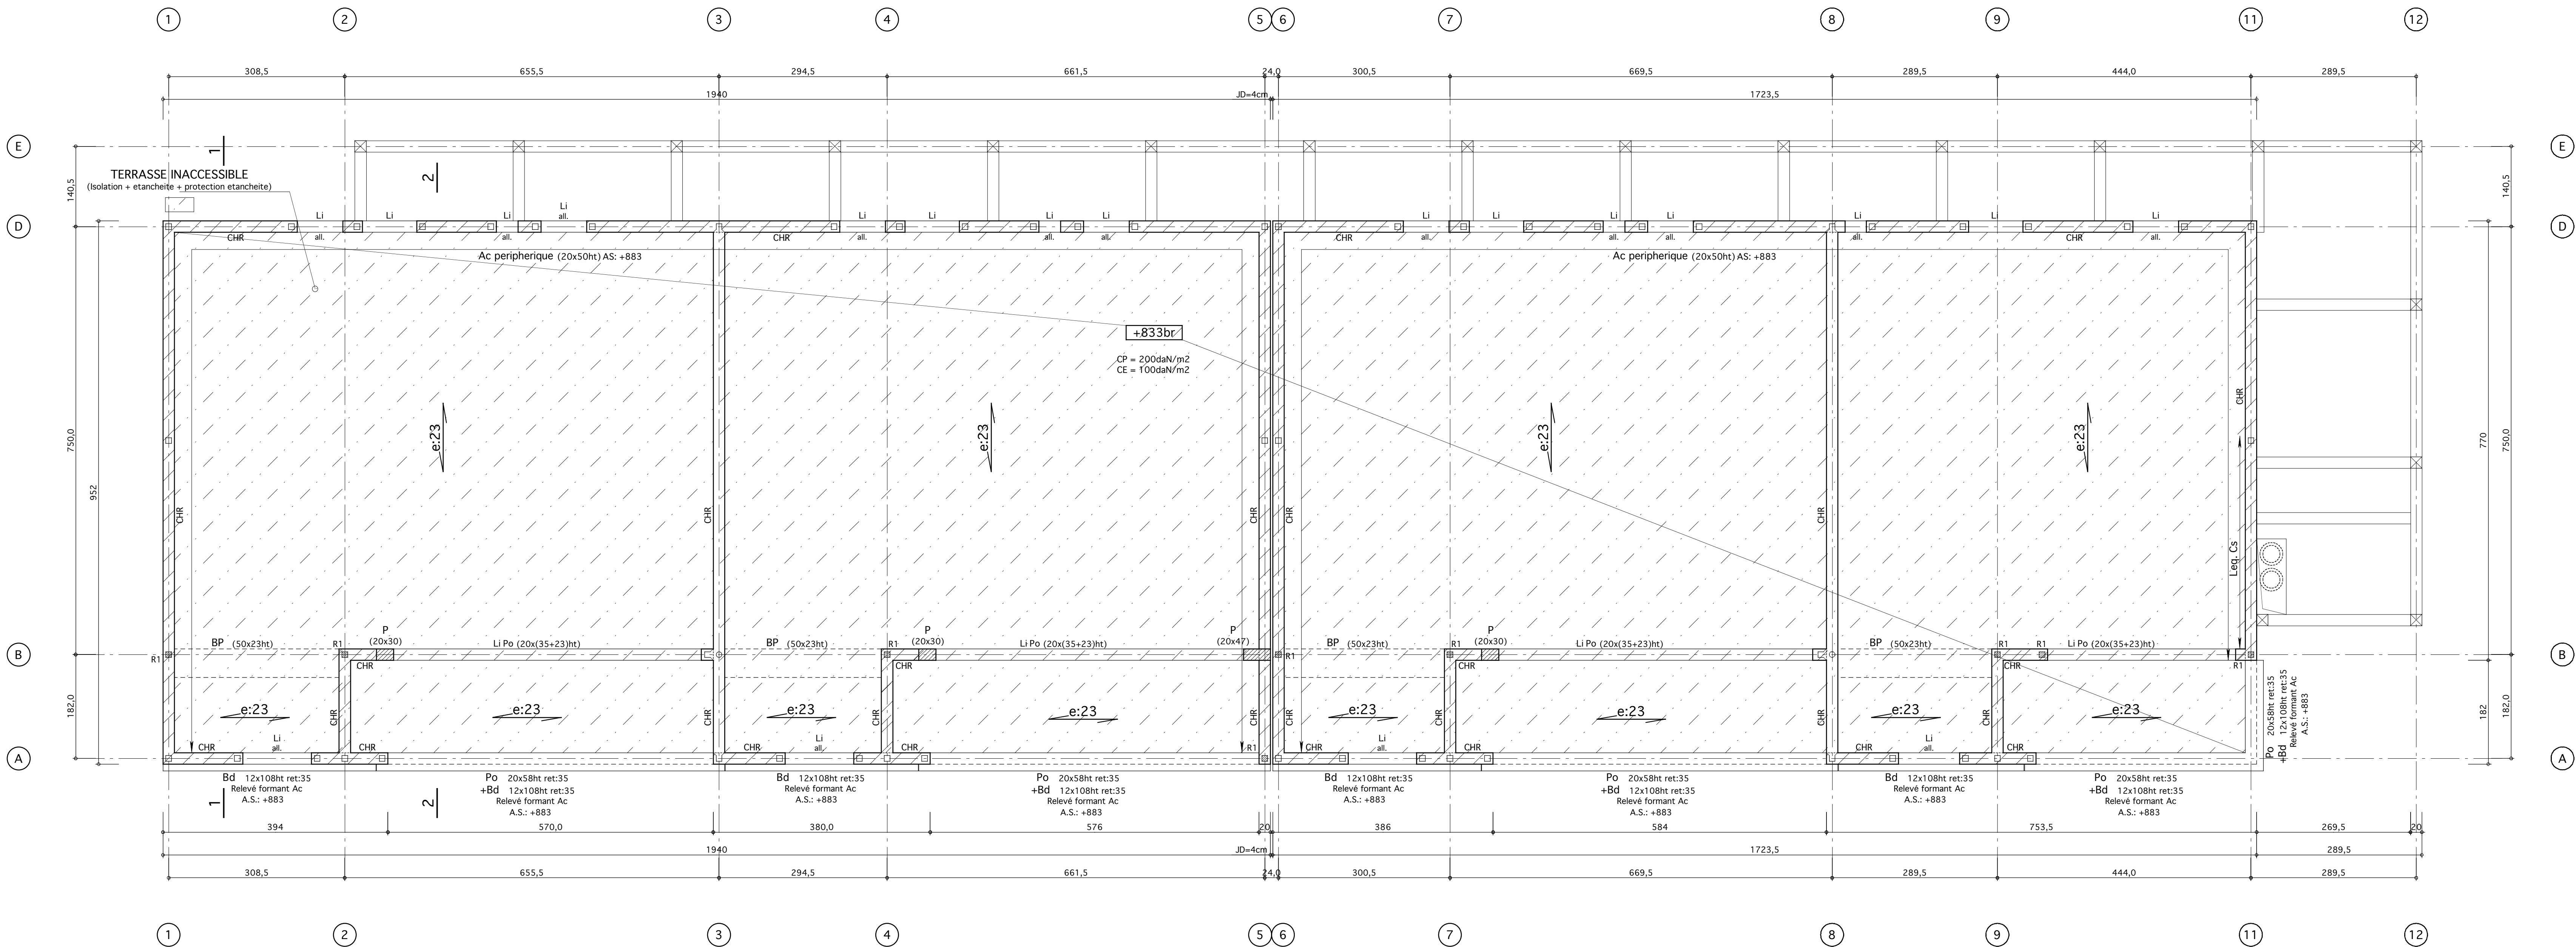

- MUR BANCHE (e:20)
- MUR MAÇONNERIE (e:20)
- RAIDISSEURS: ARMATURES 4HA10+cad. HA6 e:10
- RAIDISSEURS ARMES: ARMATURES 4HA12+cad. HA6 e:10

HYPOTHESES SISMIQUES:
. Ferrieres situe en zone sismique 3: $a_g=1,1\text{m/s}^{-2}$
. Batiment categorie d'importance 2: $\gamma_1=1$
. Sol classe E: $S=1,8$

D.C.E

commune: FERRIERES	departement: 09	Aff.: 134/18
AFFAIRE :	ACIERS: $f_e = 500\text{ MPa}$ BETON: $f_{c28} = 25\text{ MPa}$ $f_{t28} = 2,1\text{ MPa}$ dosage suivant NF 206.1	PLAN: 04
HLM DE L'ARIEGE CONSTRUCTION de 11 LOGEMENTS "Coeur de Bourg"		DATE: --/06/19 ECHELLE: 1/50
DESIGNATION :	modifications	dates
PLANCHER HAUT 2EME		indices
		EBM: "LES POUSES" Rte de Portet 31270 Villeneuve Tolosane TEL: 05.61.75.98.88 FAX: 05.61.76.79.13
Dessiné par : B. CHARPENTREAU		
M. D'OEUVRE : Architecture & Paysage	ENT. :	CONTROLE :

NOTA:
- Tous les niveaux sont donnes par rapport au $\pm 0,00$, qui correspond au sol fini du RDC.
- L'emprise des menuiseries sera a confirmer par le(s) lot(s) concerne(s).