



COUPE 1.1

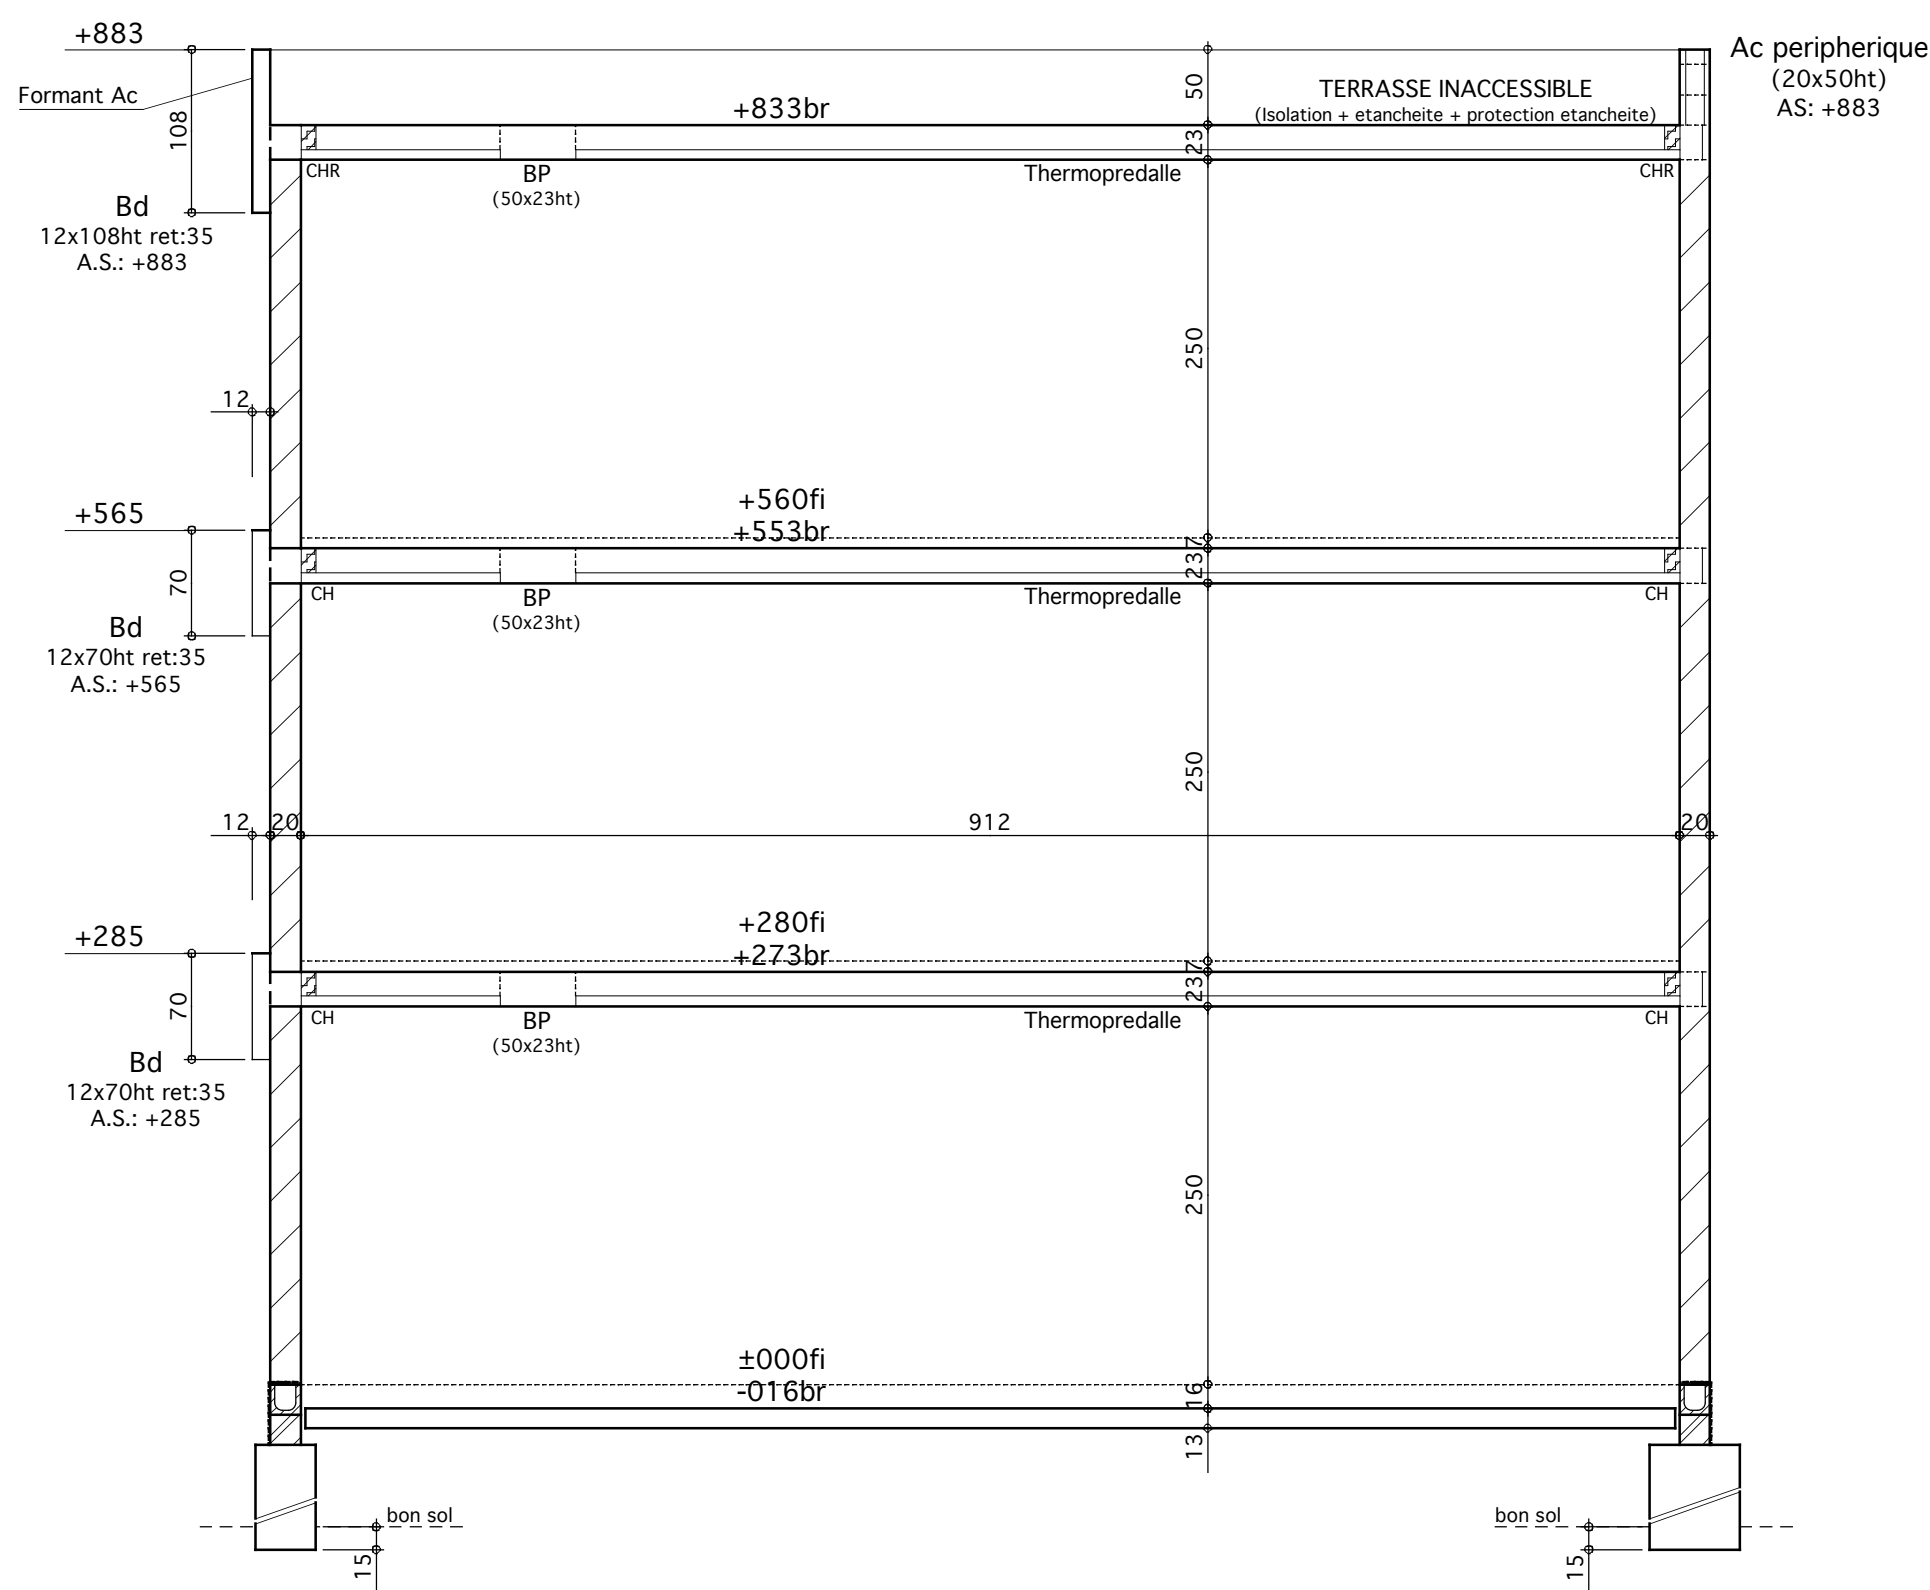

COUPE 2.2

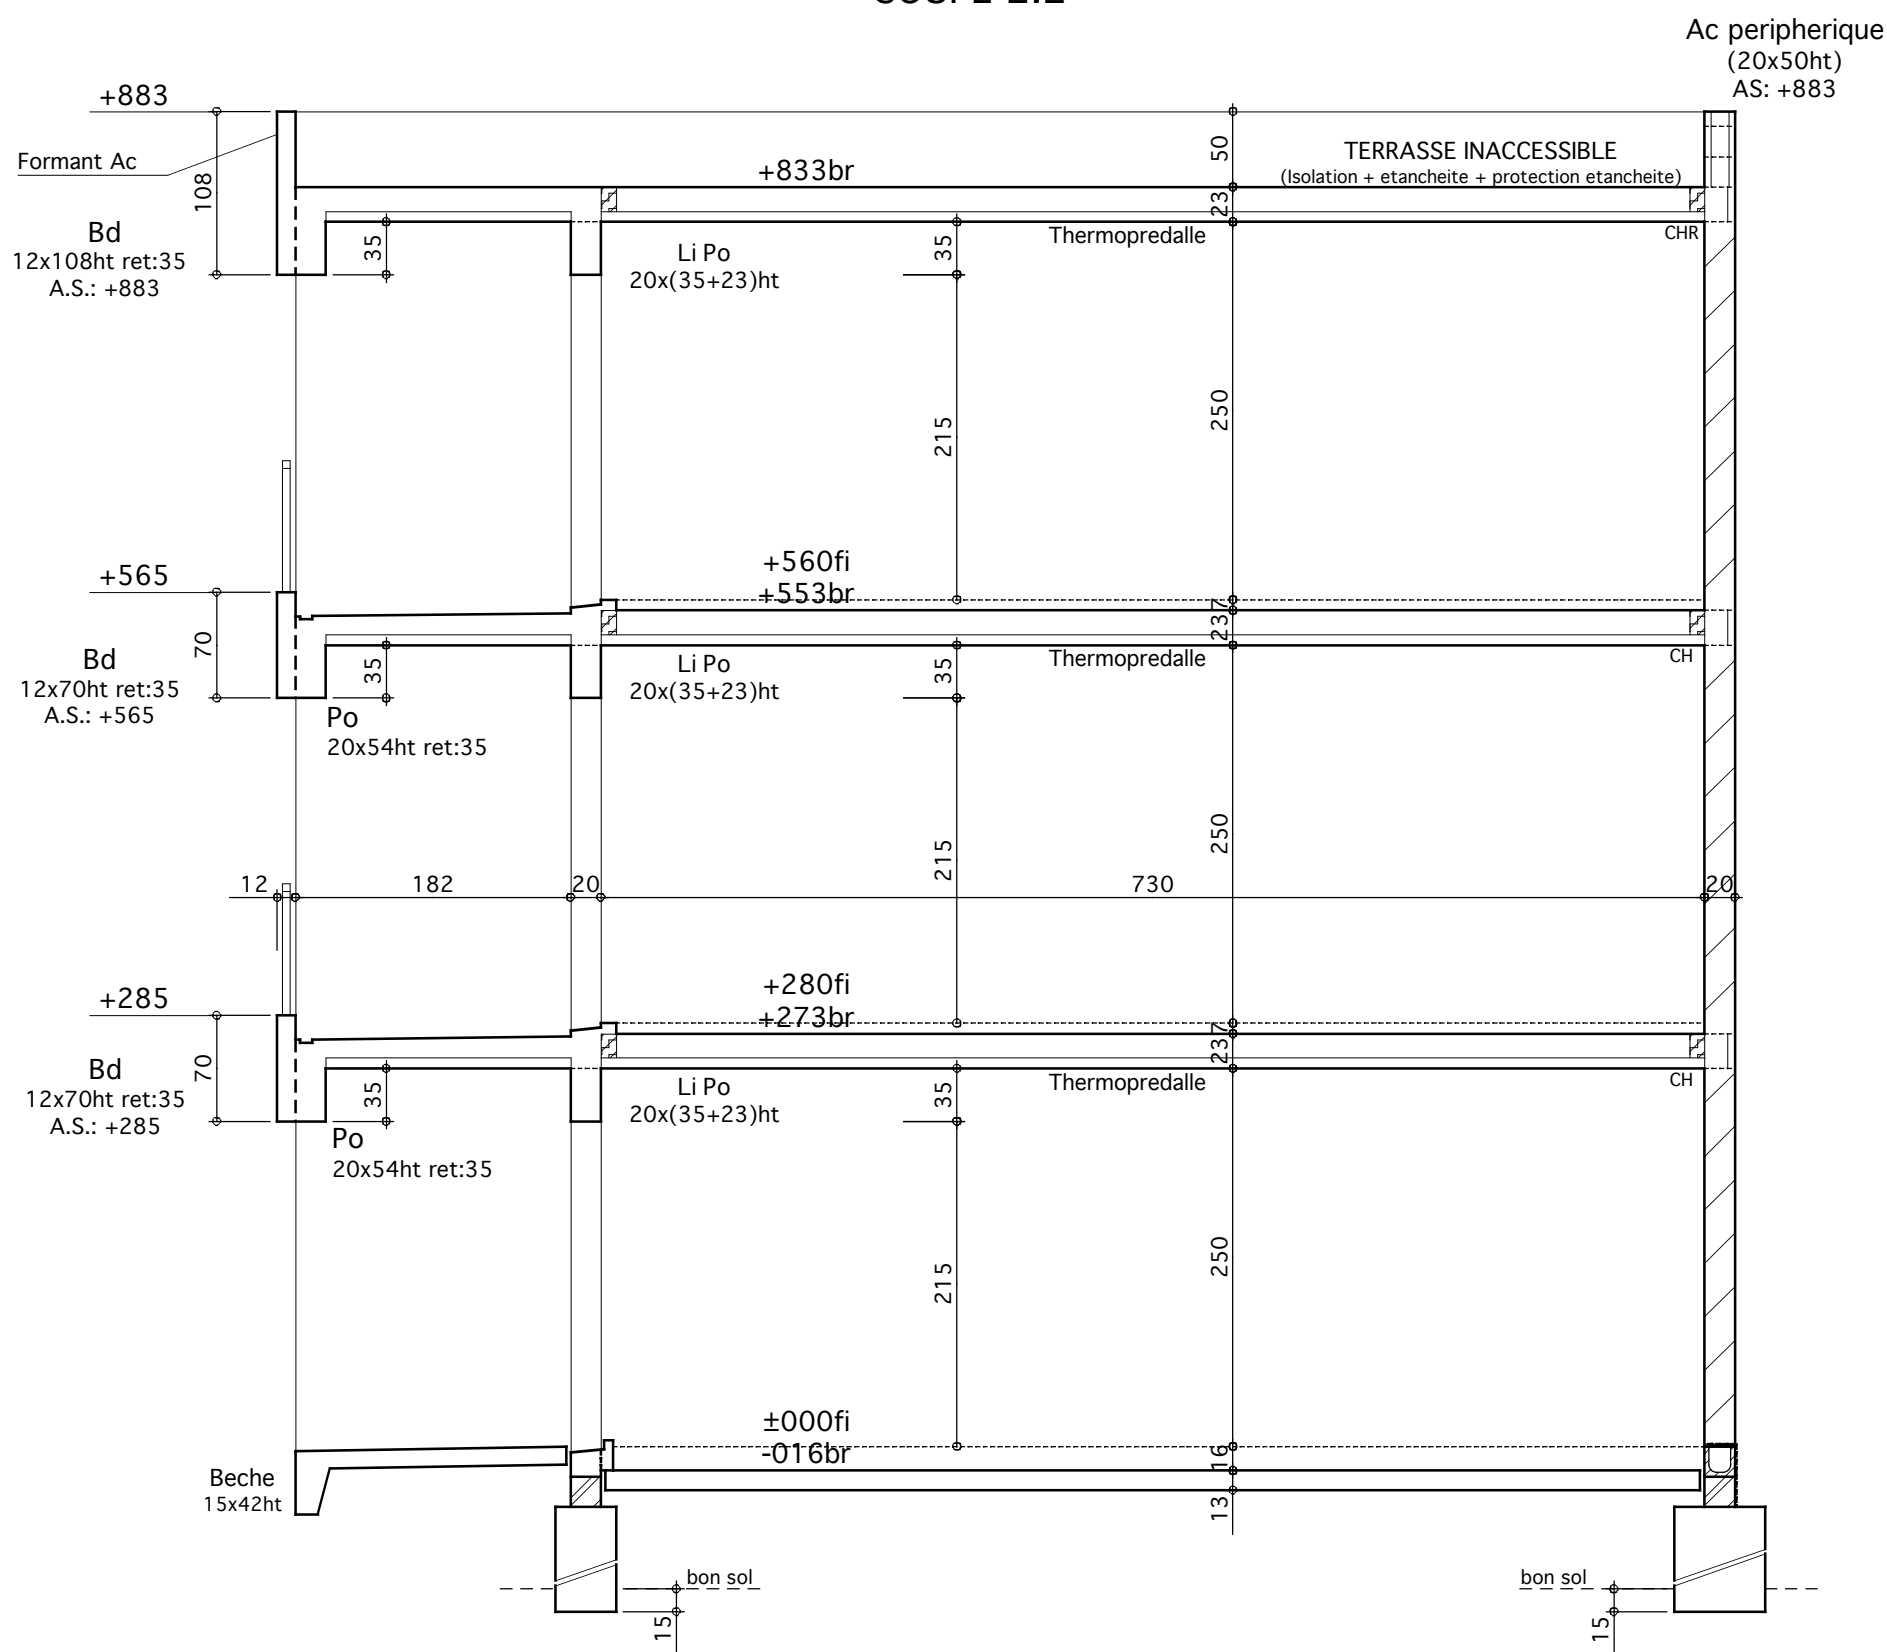

D.C.E

commune: FERRIERES	departement: 09	Aff.: 134/18
AFFAIRE : HLM DE L'ARIEGE CONSTRUCTION de 11 LOGEMENTS "Coeur de Bourg"	ACIERS: fe = 500 MPa BETON: fc28 = 25 MPa ft28 = 2,1 MPa dosage suivant NF 206.1	PLAN: 05 DATE: --/06/19 ECHELLE: 1/50
DESIGNATION : COUPES 1.1 / 2.2	modifications	dates
Dessiné par : B. CHARPENTREAU	indices	EBM: "LES POUSES" Rte de Portet 31270 Villeneuve Tolosane TEL: 05.61.76.98.88 FAX: 05.61.76.79.13
M. D'OEUVRE : Architecture & Paysage	ENT. :	CONTROLE :

