
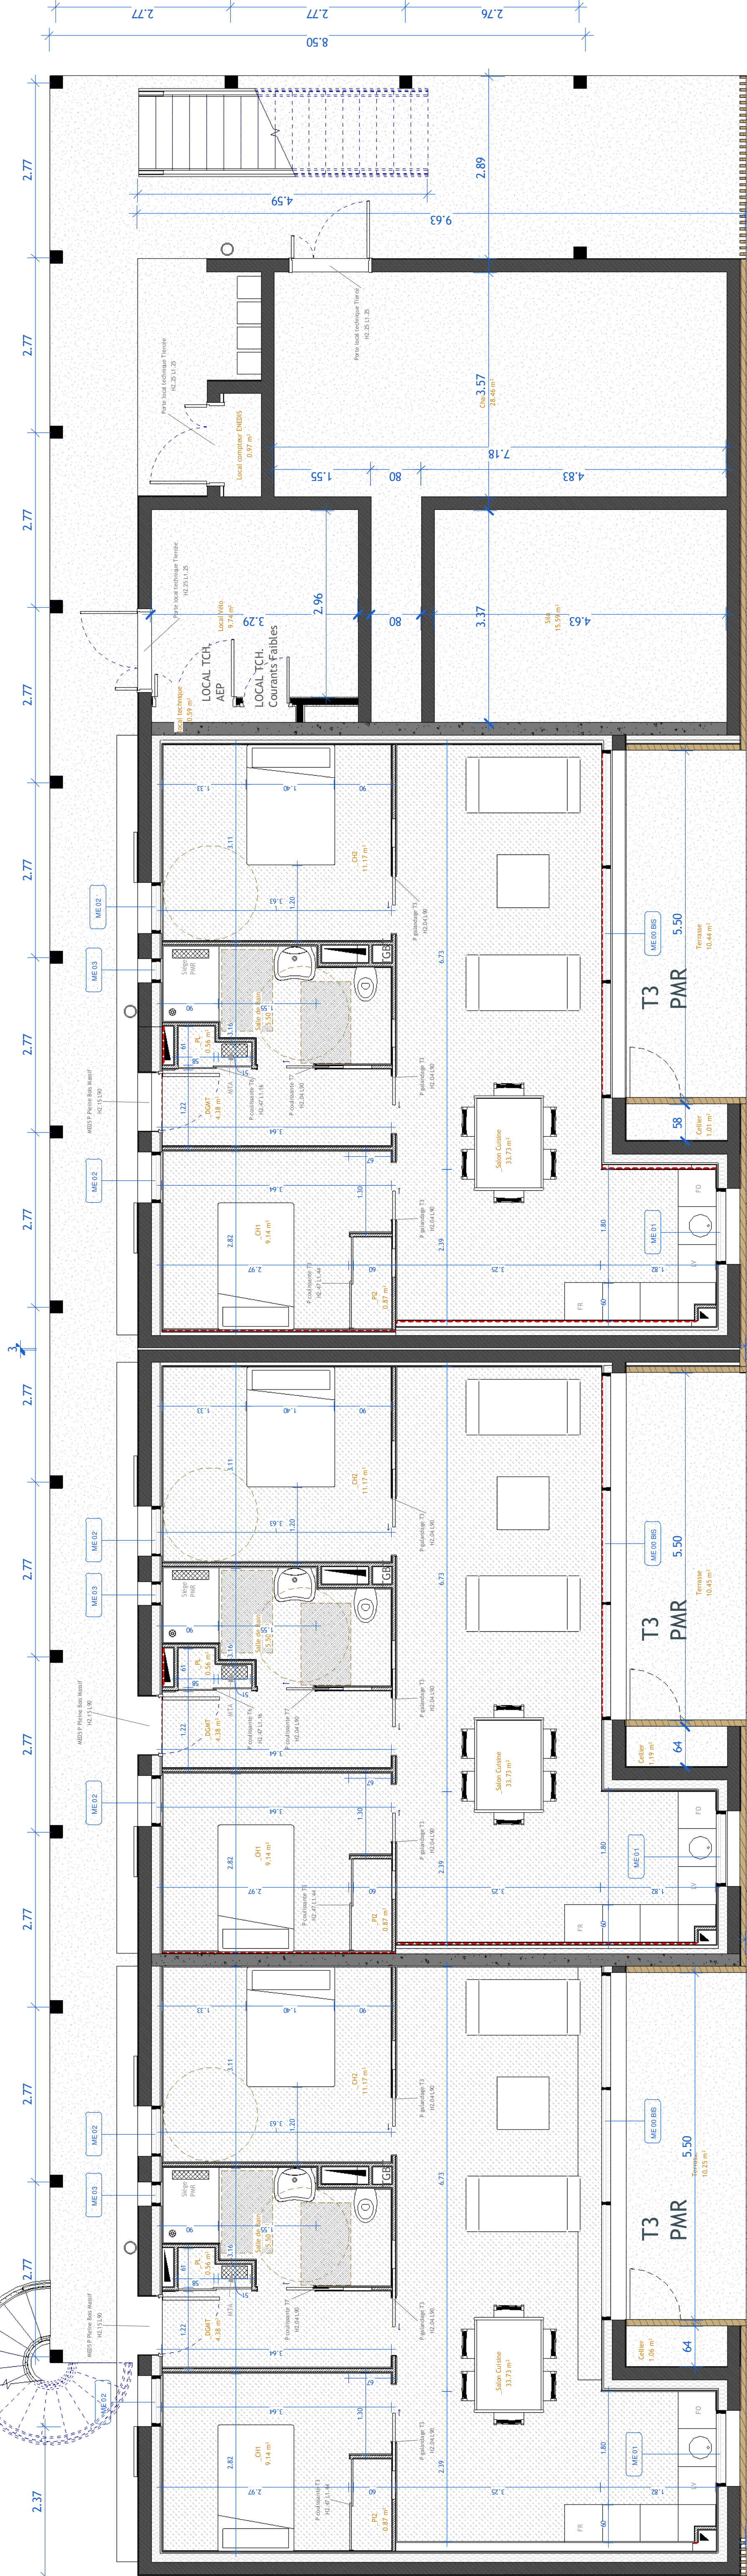


36.70

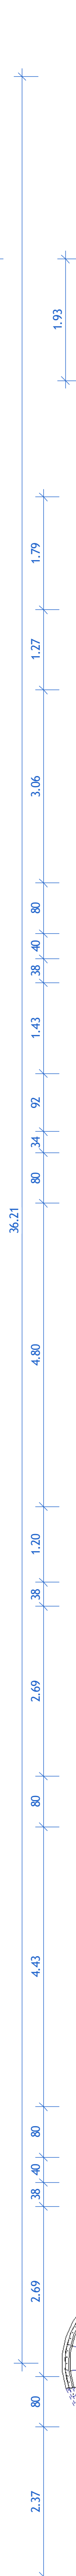

CONSTRUCTION DE 11 LOGEMENTS DANS LE CENTRE
BOURG DE FERRIERES SUR ARIEGE

Maitrise d'ouvrage
OPH de l'Ariège
23 b rue de Ferrières
BP 500 39

APS APD PRO ACT EXE DET AOR

Maitrise d'oeuvre :

ARCHITECTURE ET PAYSAGE sarl
63 65 Rue Jean Jaurès
09300 LA VELANET
Tel: 05 61 03 52 61 Fax: 05 61 03 52 97

ESI
7 Avenue du 8 Mai 1945
09120 VARHILES
Tel: 05 61 60 86 99 Fax: 09 70 62 86 98

EBM
Les poussees
Rte de portet
31270 villeneuve tolosane
Tel : 05 61 76 98 88

ACM
acm@acm-sarl.fr
05 62 30 83 33
2 rue Jules Vâdrines
31400 TOULOUSE

APAVE FOIX - David Mariani
05 61 65 29 31
foix@apave.com
3, avenue de Paris
09330 Montgallard

Assistance
Coordination
Maitrise d'œuvre

apave

Echelle 1 : 50
Format Papier A1

PLAN NIVEAU 0

Version 1
13/06/2019 18:11:49