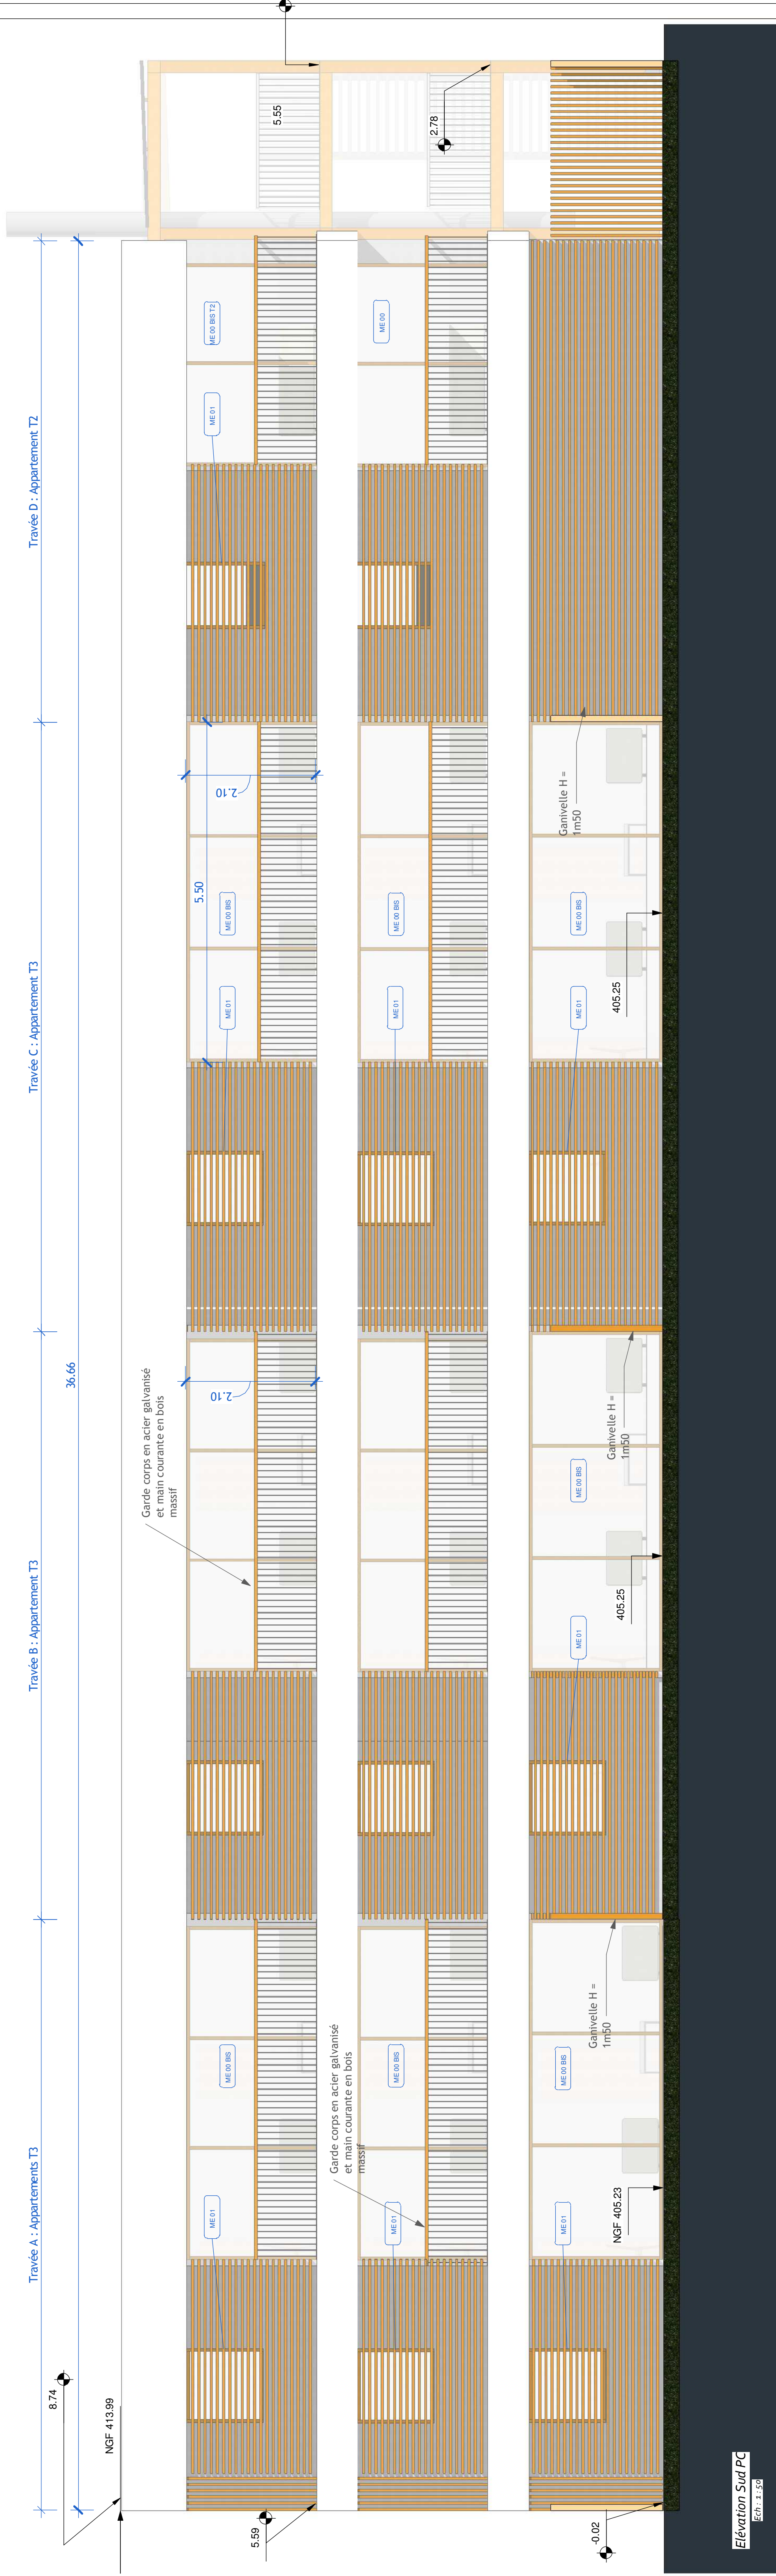




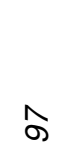
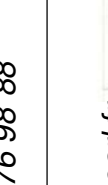
**CONSTRUCTION DE 11 LOGEMENTS DANS LE CENTRE
BOURG DE FERRIERES SUR ARIEGE**

Maîtrise d'ouvrage

OPH de l'Ariège
23 b rue de Ferrières
BP 500 39

APS	APD	PRO	ACT	EXE	DET	AOR
-----	-----	------------	-----	-----	-----	-----

Maîtrise d'oeuvre :

 ARCHITECTURE ET PAYSAGE sarl 63,65 Rue Jean Jaurès 09300 VILLELANET Tel : 05 61 03 52 61 Fax: 05 61 03 52 97	ESI 7, Avenue du 8 Mai 1945 09120 VARRHELES Tel : 05 61 60 86 99 Fax: 09 70 62 86 98	EBM Les pousses Rte de portet 31270 villeneuve tolosane Tel : 05 61 76 98 88	ACM acm@acm-sarl.fr 05 62 30 83 33 2 rue Jules Verlines 31400 TOULOUSE
 Assistance Coordination Maîtrise d'œuvre	apave systèmes ingénierie environnement - matériaux - usages	Bureau d'Etudes ebm 	apave 
APAVE FOX - David Mariani 05 61 65 29 31 loix@apave.com 3, avenue de Paris 09330 Montgallard			

Echelle 1 : 50
Format Papier A1

Façade Sud Bardée

Version 1
13/06/2019 18:12:04