


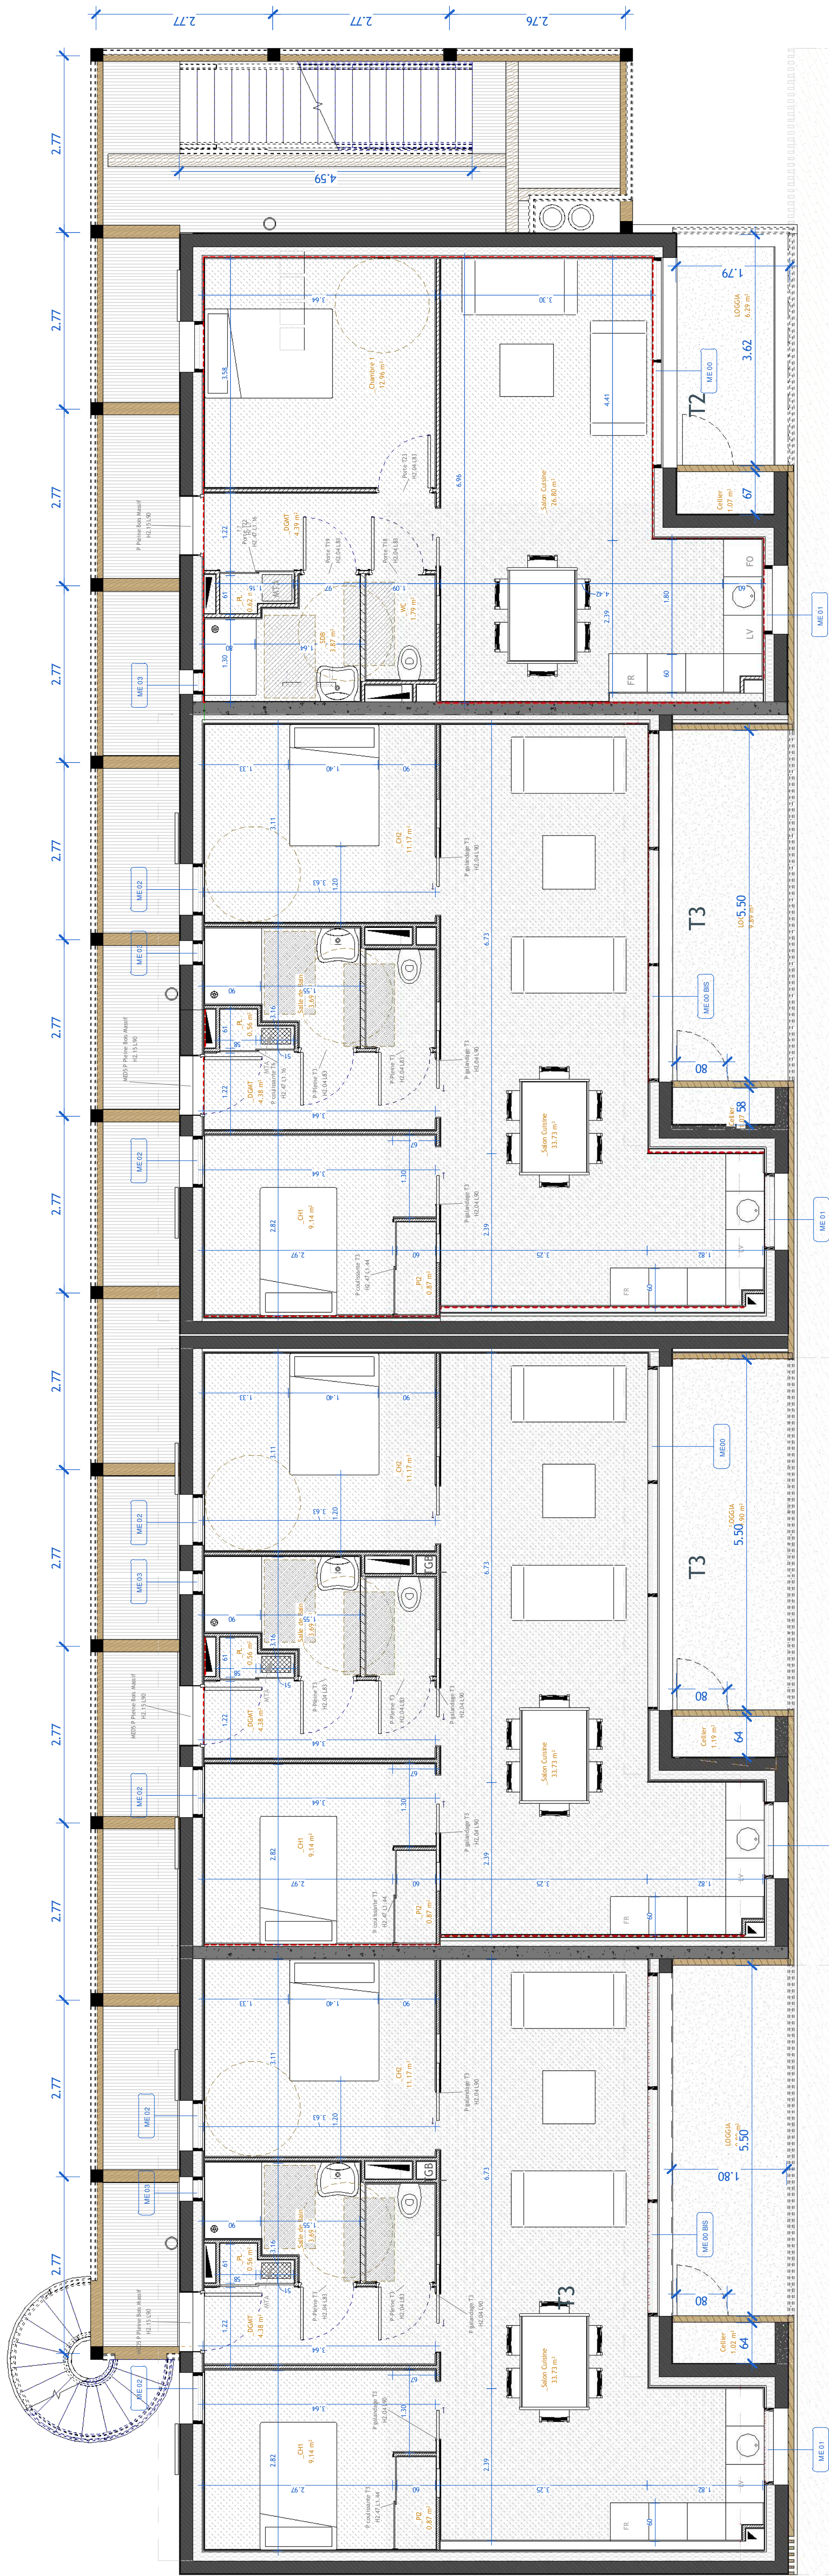

**CONSTRUCTION DE 11 LOGEMENTS DANS LE CENTRE
BOURG DE FERRIERES SUR ARIEGE**

Maîtrise d'ouvrage

OPH de l'Ariège
23 b rue de Ferrières
BP 500 39

APS	APD	PRO	ACT	EXE	DET	AOR
-----	-----	------------	-----	-----	-----	-----

Maîtrise d'oeuvre :

 ARCHITECTURE ET PAYSAGE sarl 63 65 Rue Jean Jaurès 09300 LAVELANET Tel: 05 61 03 52 61 Fax: 05 61 03 52 97	 ESi énergie des Pyrénées ingénierie environnementale 7, Avenue du 8 Mai 1945 09120 VARRILLES Tel: 05 61 00 86 99 Fax: 09 70 62 86 98	 EBM Les pousses Rte de portlet 31270 villeneuve tolosane Tel : 05 61 76 98 88	 Assistance Coordination Maîtrise d'œuvre  ACM acm@acm-sarl.fr 05 62 30 83 33 2 rue Jules Védrières 31400 TOULOUSE	 APAVE FOIX - David Martani 05 61 65 29 31 toix@apave.com 3, avenue de Paris 09330 Montgallard
---	---	---	--	---

PLAN NIVEAU 1

Version 1
13/06/2019 18:11:51