


Conduit d'évacuation de fumée de la
chaufferie

8.74

Couverture polycarbonate type onduline PC
Panne Bois massif section 200 mm x 100 mm en support de la couverture en onduline
Poutre Bois massif section 200 mm x 200 mm reprise dans la
maçonnerie

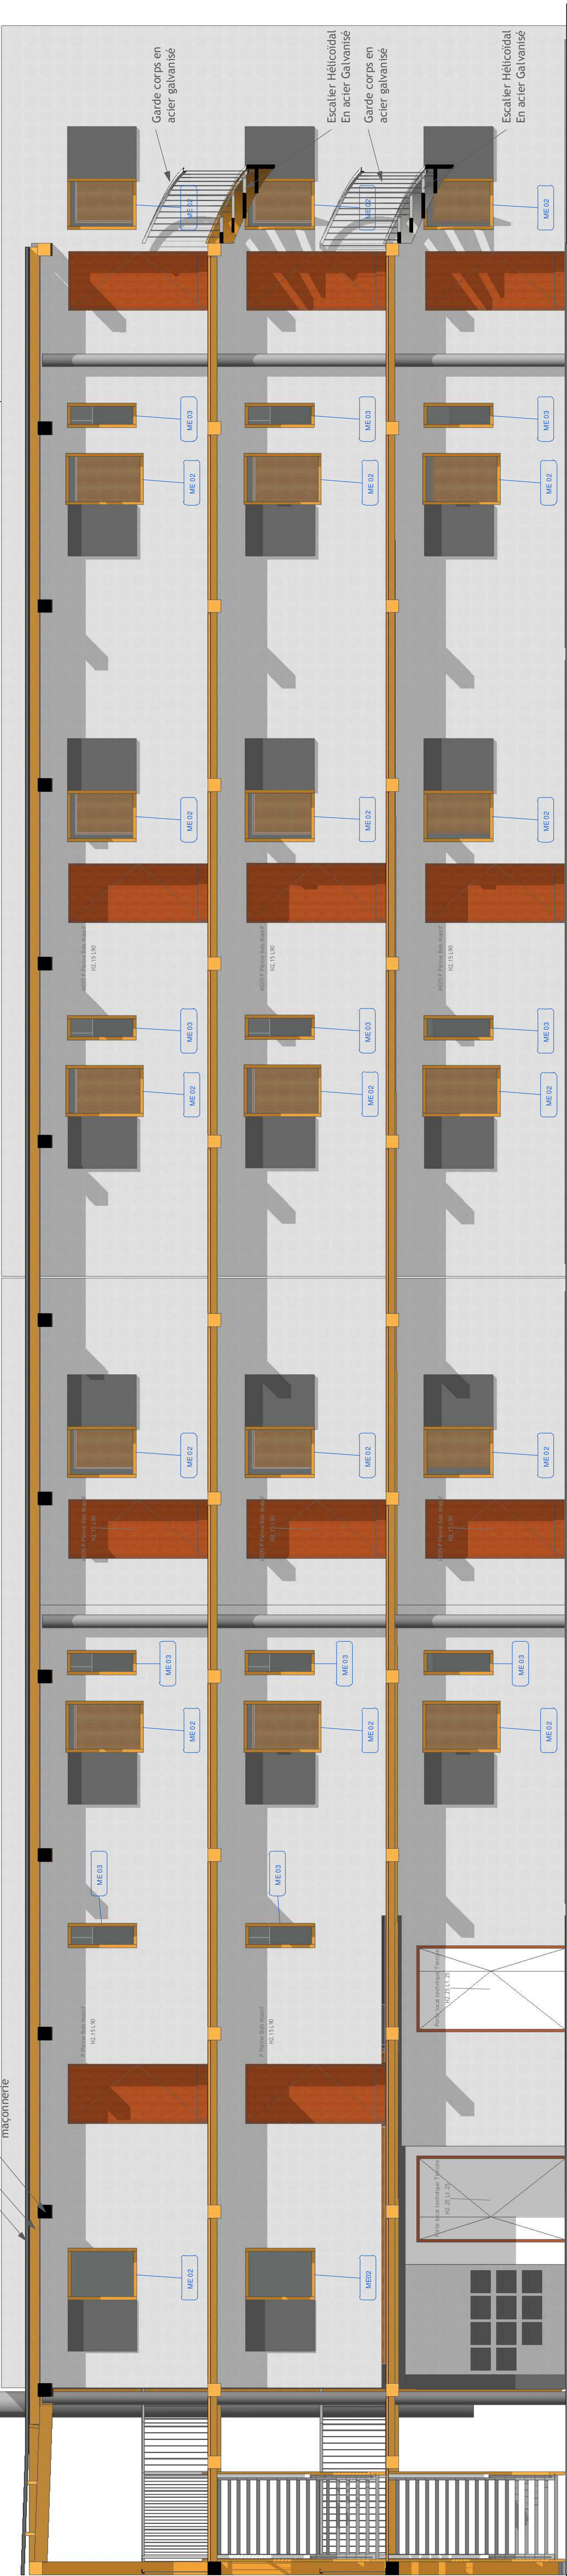

Elévation Nord PC Copie 1
Ech : 1 : 50

CONSTRUCTION DE 11 LOGEMENTS DANS LE CENTRE
BOURG DE FERRIERES SUR ARIEGE

Maitrise d'ouvrage

OPH de l'Ariège
23 b rue de Ferrières
BP 500 39

APS	APD	PRO	ACT	EXE	DET	AOR
-----	-----	-----	-----	-----	-----	-----

Maitrise d'oeuvre :

 ARCHITECTURE ET PAYSAGE sarl 63 65 Rue Jean Jaurès 09300 LA VELANET Tel: 05 61 03 52 61 Fax: 05 61 03 52 97	 ESI 7 Avenue du 8 Mai 1945 09120 VARHILES Tel: 05 61 60 86 99 Fax: 09 70 62 86 98	 EBM Les poussees Rte de porret 31270 Villeneuve tolosane Tel : 05 61 76 98 88	 ACM acm@acm-sarl.fr 05 62 30 83 33 2 rue Jules Vâdrines 31400 TOULOUSE	 APAVE 05 61 65 29 31 foix@apave.com 3, avenue de Paris 09330 Montgallard
---	---	--	---	---

Echelle 1 : 50
Format Papier A1

Elevation Façade
maçonnée
Version 1
13/06/2019 18:11:55