
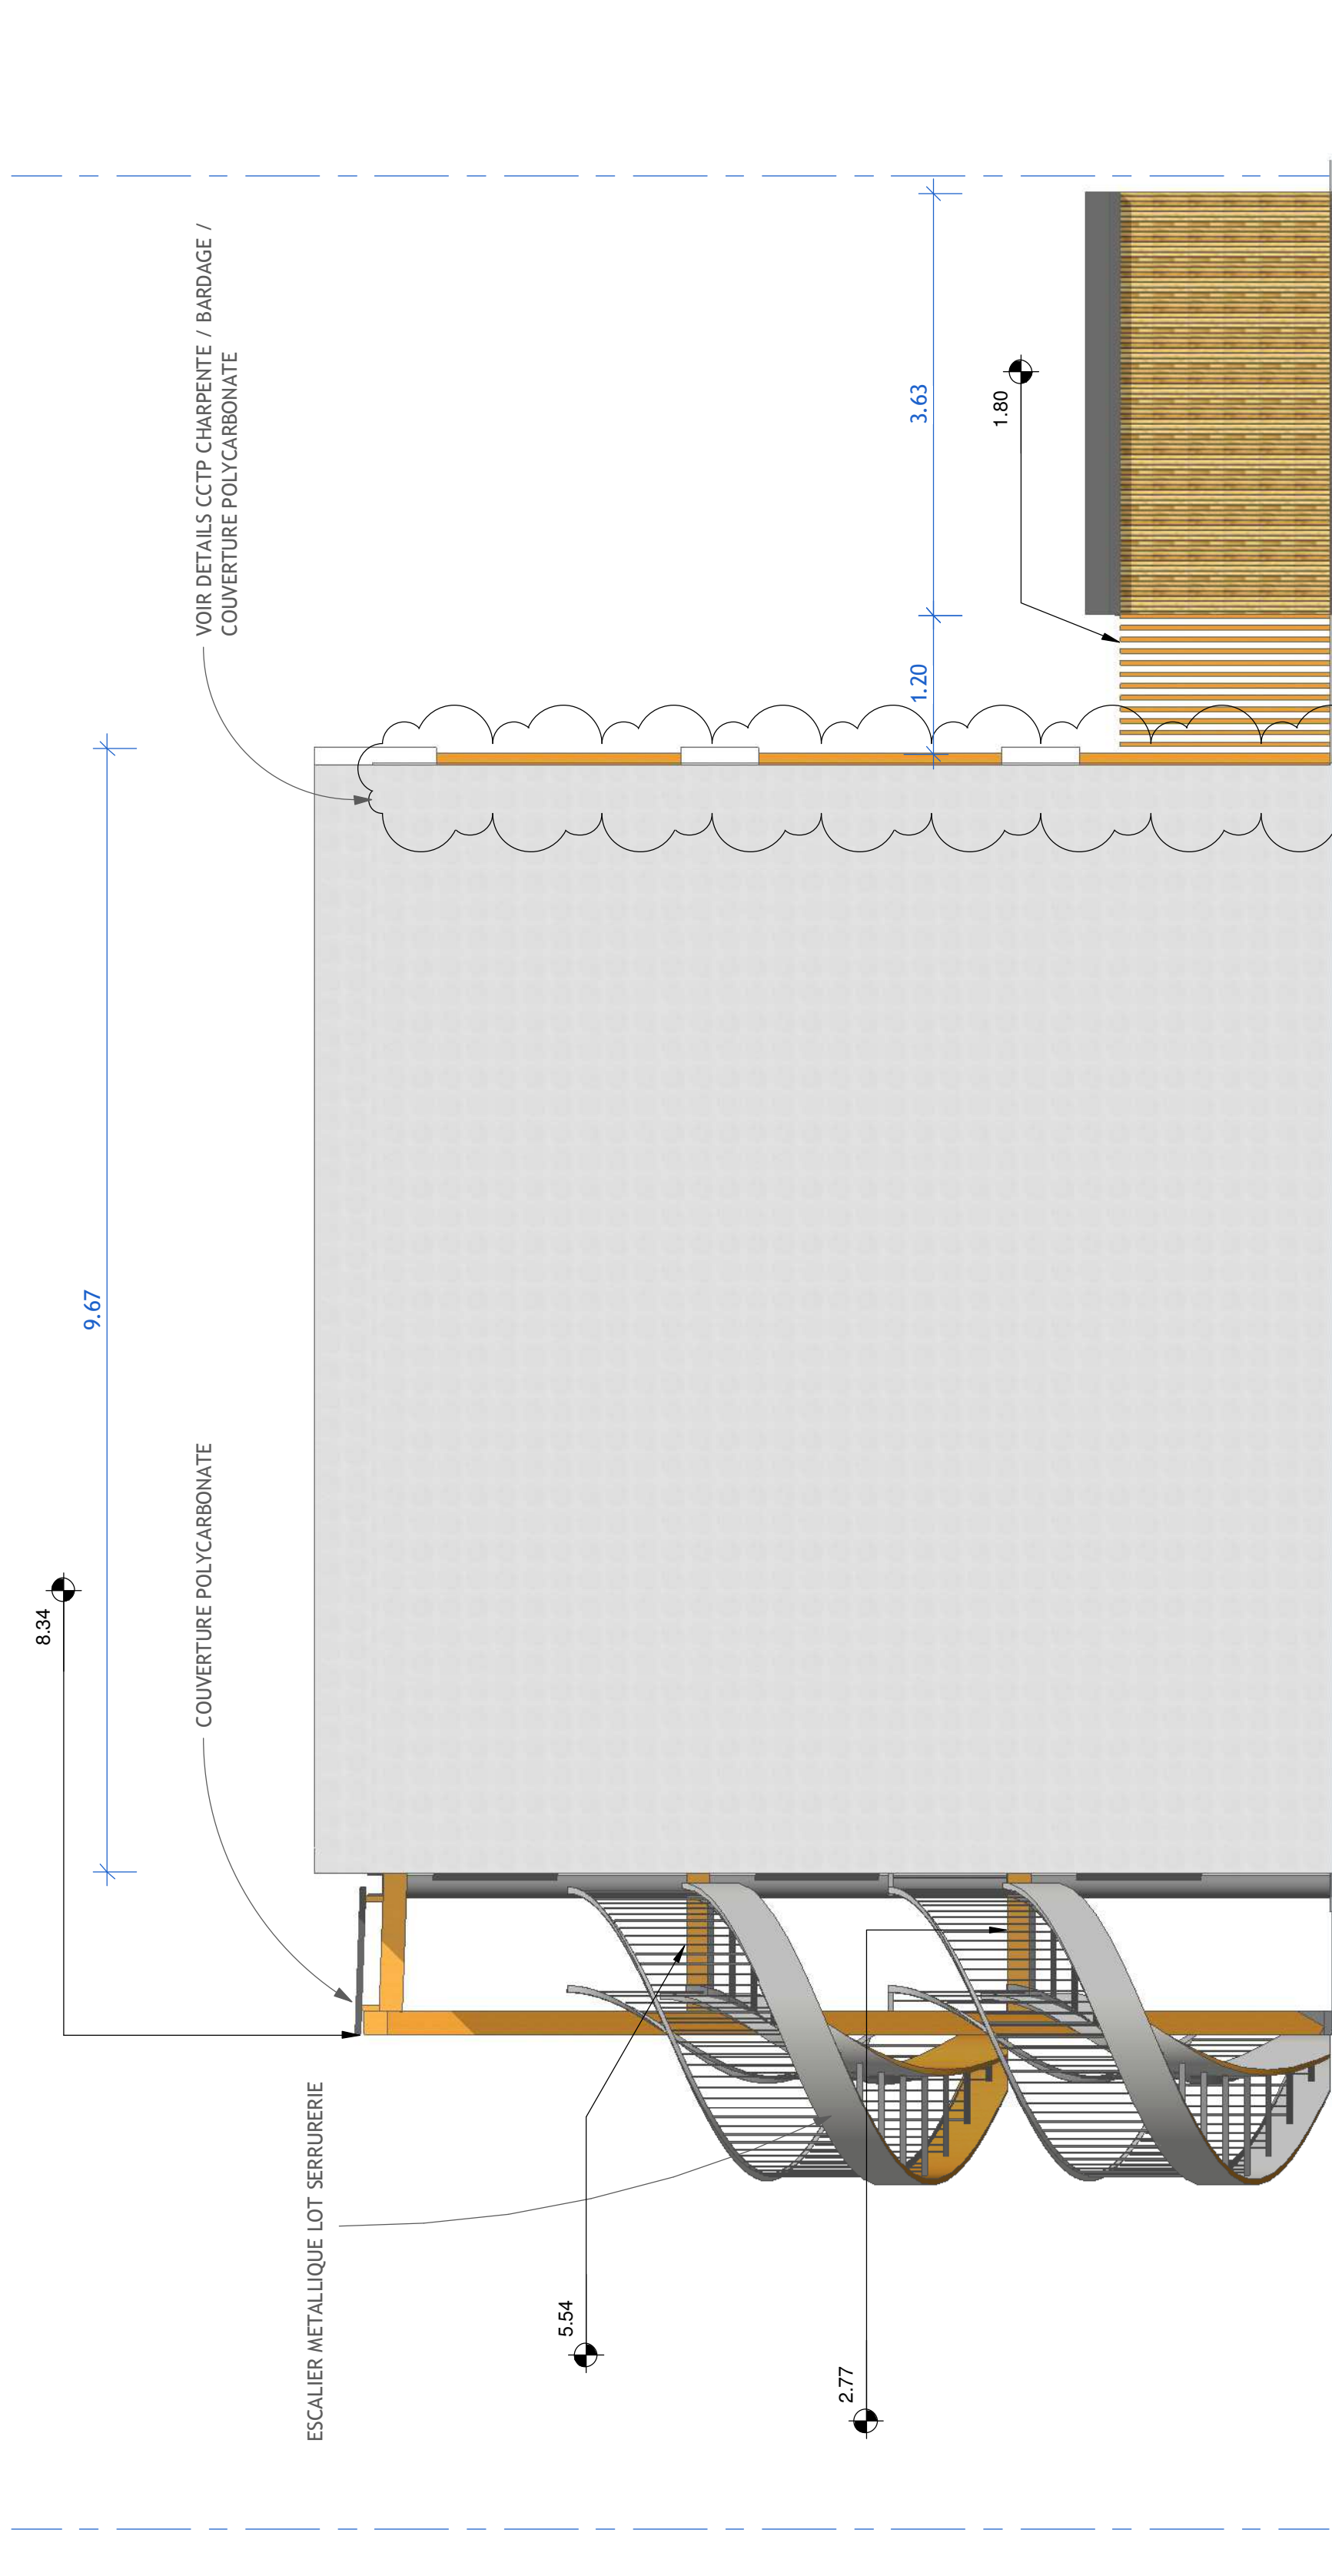


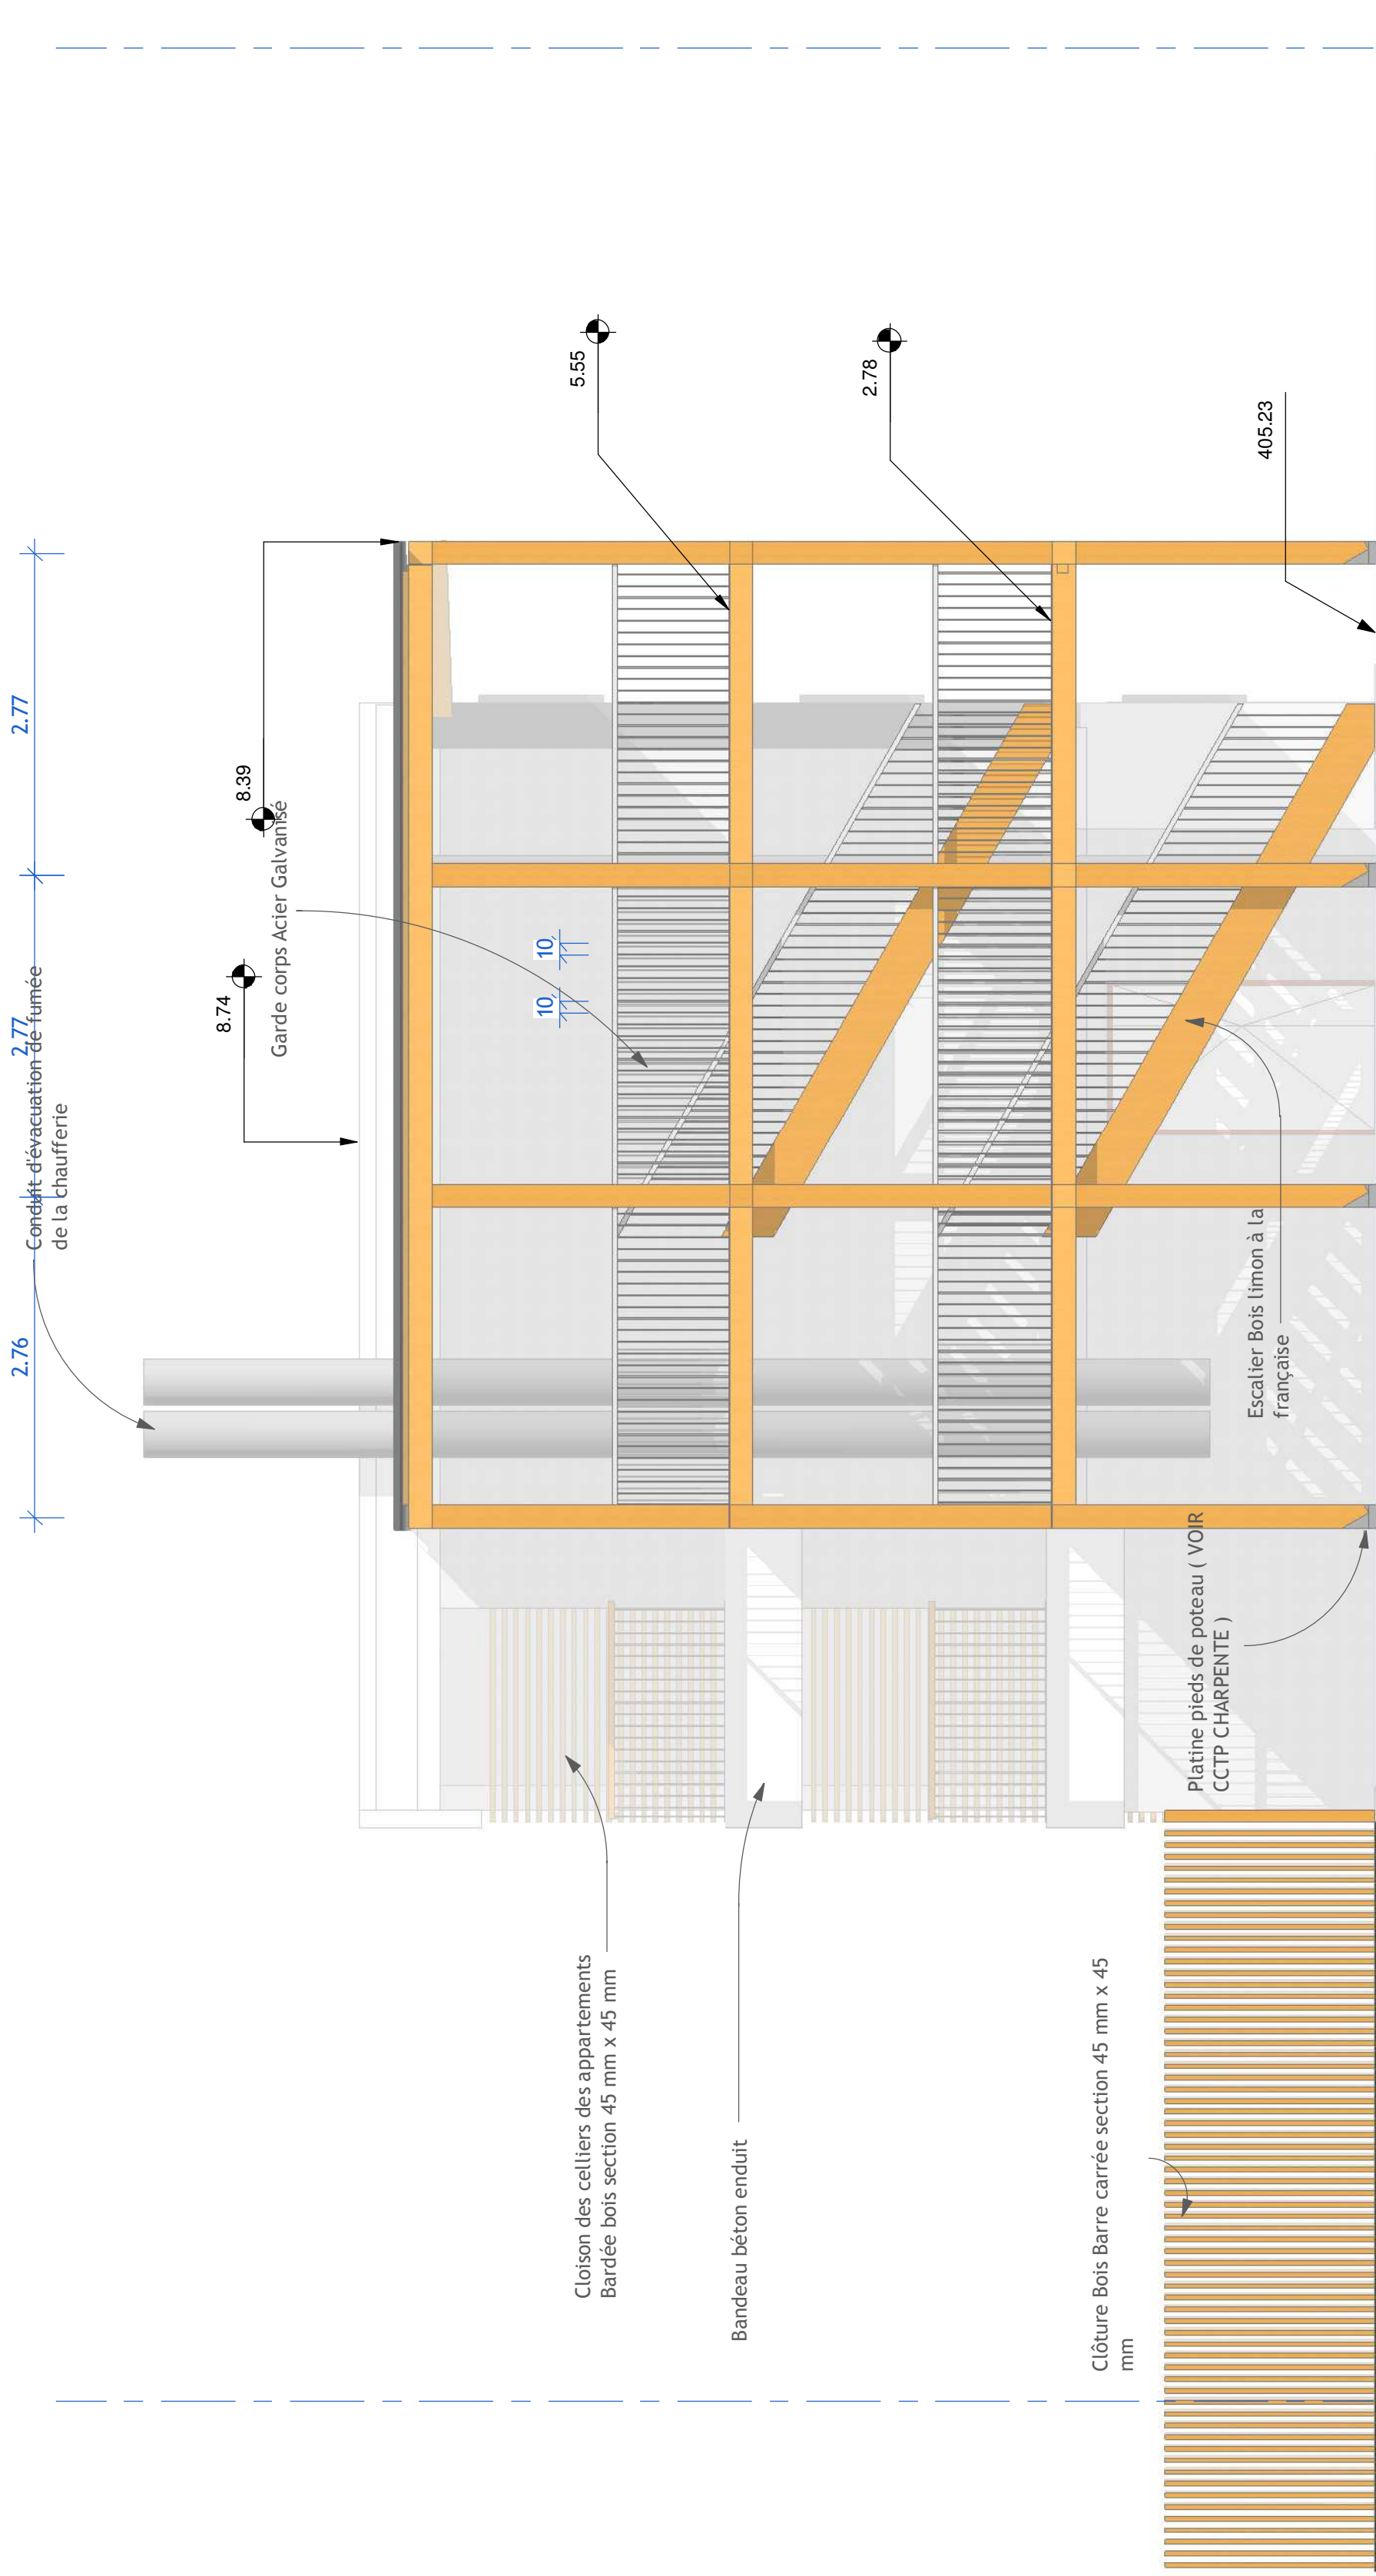

CONSTRUCTION DE 11 LOGEMENTS DANS LE CENTRE <u>BOURG DE FERRIERES SUR ARIEGE</u>			
<u>Maîtrise d'ouvrage</u> OPH de l'Ariège 23 b rue de Ferrières BP 500 39			
APS	APD	PRO	ACT EXE DET AOR
<u>Maîtrise d'oeuvre :</u>			
 ARCHITECTURE ET PAYSAGE sarl 63 65 Rue Jean Jaurès 09300 LA VELANET Tel: 05 61 03 52 61 Fax: 05 61 03 52 97			
 ESI 7 Avenue du 8 Mai 1945 09120 VARHILES Tel: 05 61 60 86 99 Fax: 09 70 62 86 98			
 EBM Les poussees Rte de portet 31270 Villeneuve tolosane Tel : 05 61 76 98 88			
 acm acm@acm-sarl.fr 05 62 30 83 33 2 rue Jules Vâdrines 31400 TOULOUSE			
 apave APAVE FOIX - David Mariani 05 61 65 29 31 foix@apave.com 3, avenue de Paris 09330 Montgallard			
Echelle 1 : 50 Format Papier A1			
Elevation Est et Ouest Version 1 13/06/2019 18:11:58			