

Poutre Bois
massif section
200 mm x 200
mm


Contreventements tirants
métalliques
profilé rond

Poutre Bois
massif section
200 mm x 200
mm

Poteaux Bois
massif section
200 mm x 200
mm

Escalier
hélicoïdal en
Acier Galvanisé
avec Garde
corps en acier

Contreventements tirants
métalliques
profilé rond

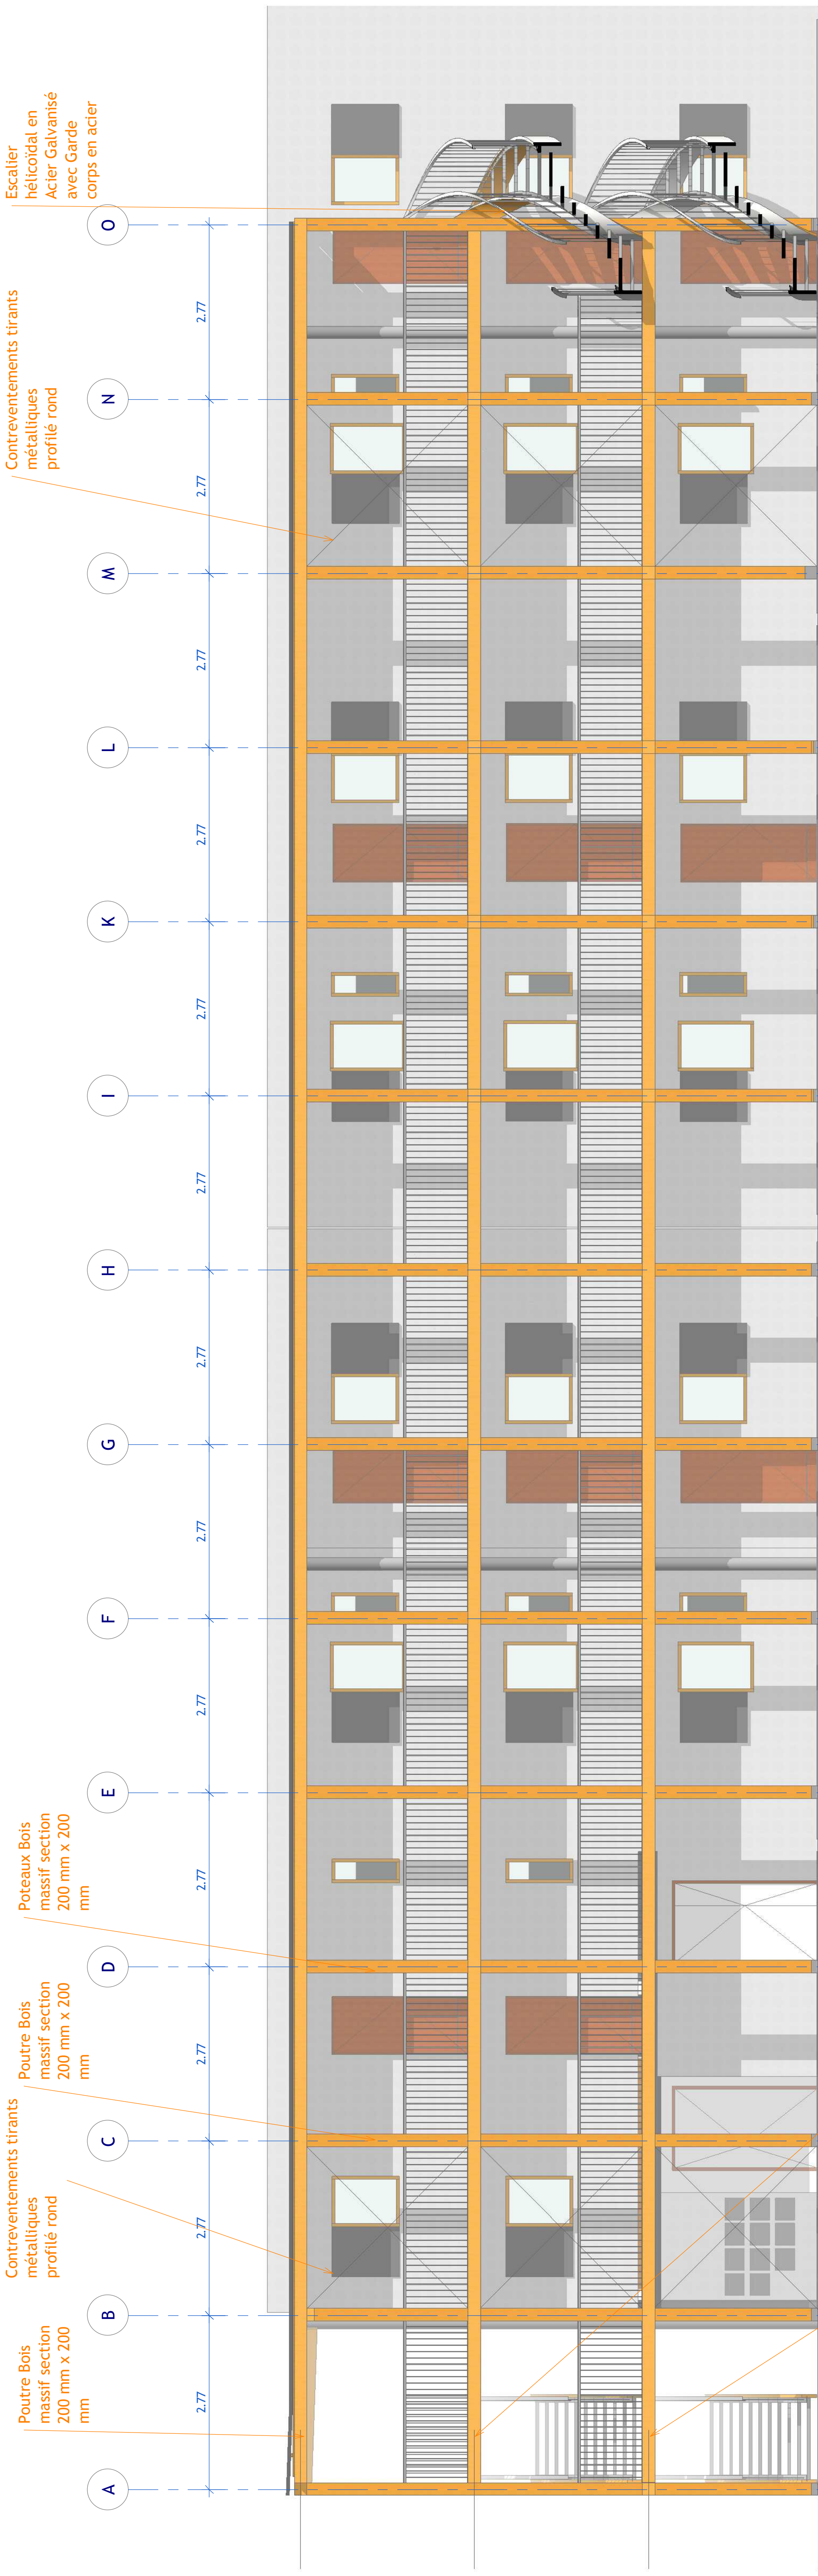

Elevation Nord PC
Echelle : 1 : 50

CONSTRUCTION DE 11 LOGEMENTS DANS LE CENTRE
BOURG DE FERRIERES SUR ARIEGE

Maîtrise d'ouvrage				
OPH de l'Ariège 23 b rue de Ferrières BP 500 39				
APS	APD	PRO	ACT	EXE DET AOR

Maîtrise d'oeuvre :



ARCHITECTURE ET PAYSAGE sarl
63 65 Rue Jean Jaurès
09300 LA VELANET
Tel: 05 61 03 52 61 Fax: 05 61 03 52 97



ESI
7 Avenue du 8 Mai 1945
09120 VARHILES
Tel: 05 61 60 86 99 Fax: 09 70 62 86 98



EBM
Les pousées
Rte de porret
31270 Villeneuve tolosane
Tel : 05 61 76 98 88



ACM
acm@acm-sarl.fr
05 62 30 83 33
2 rue Jules Vâdrines
31400 TOULOUSE



APAVE
05 61 65 29 31
foix@apave.com
3, avenue de Paris
09330 Montgallard